HONDURAS 1:50,000

BONITO ORIENTAL

EDITION 2–DMA
EDICIÓN

SERIES E752
SERIE

SHEET 3063 II
HOJA

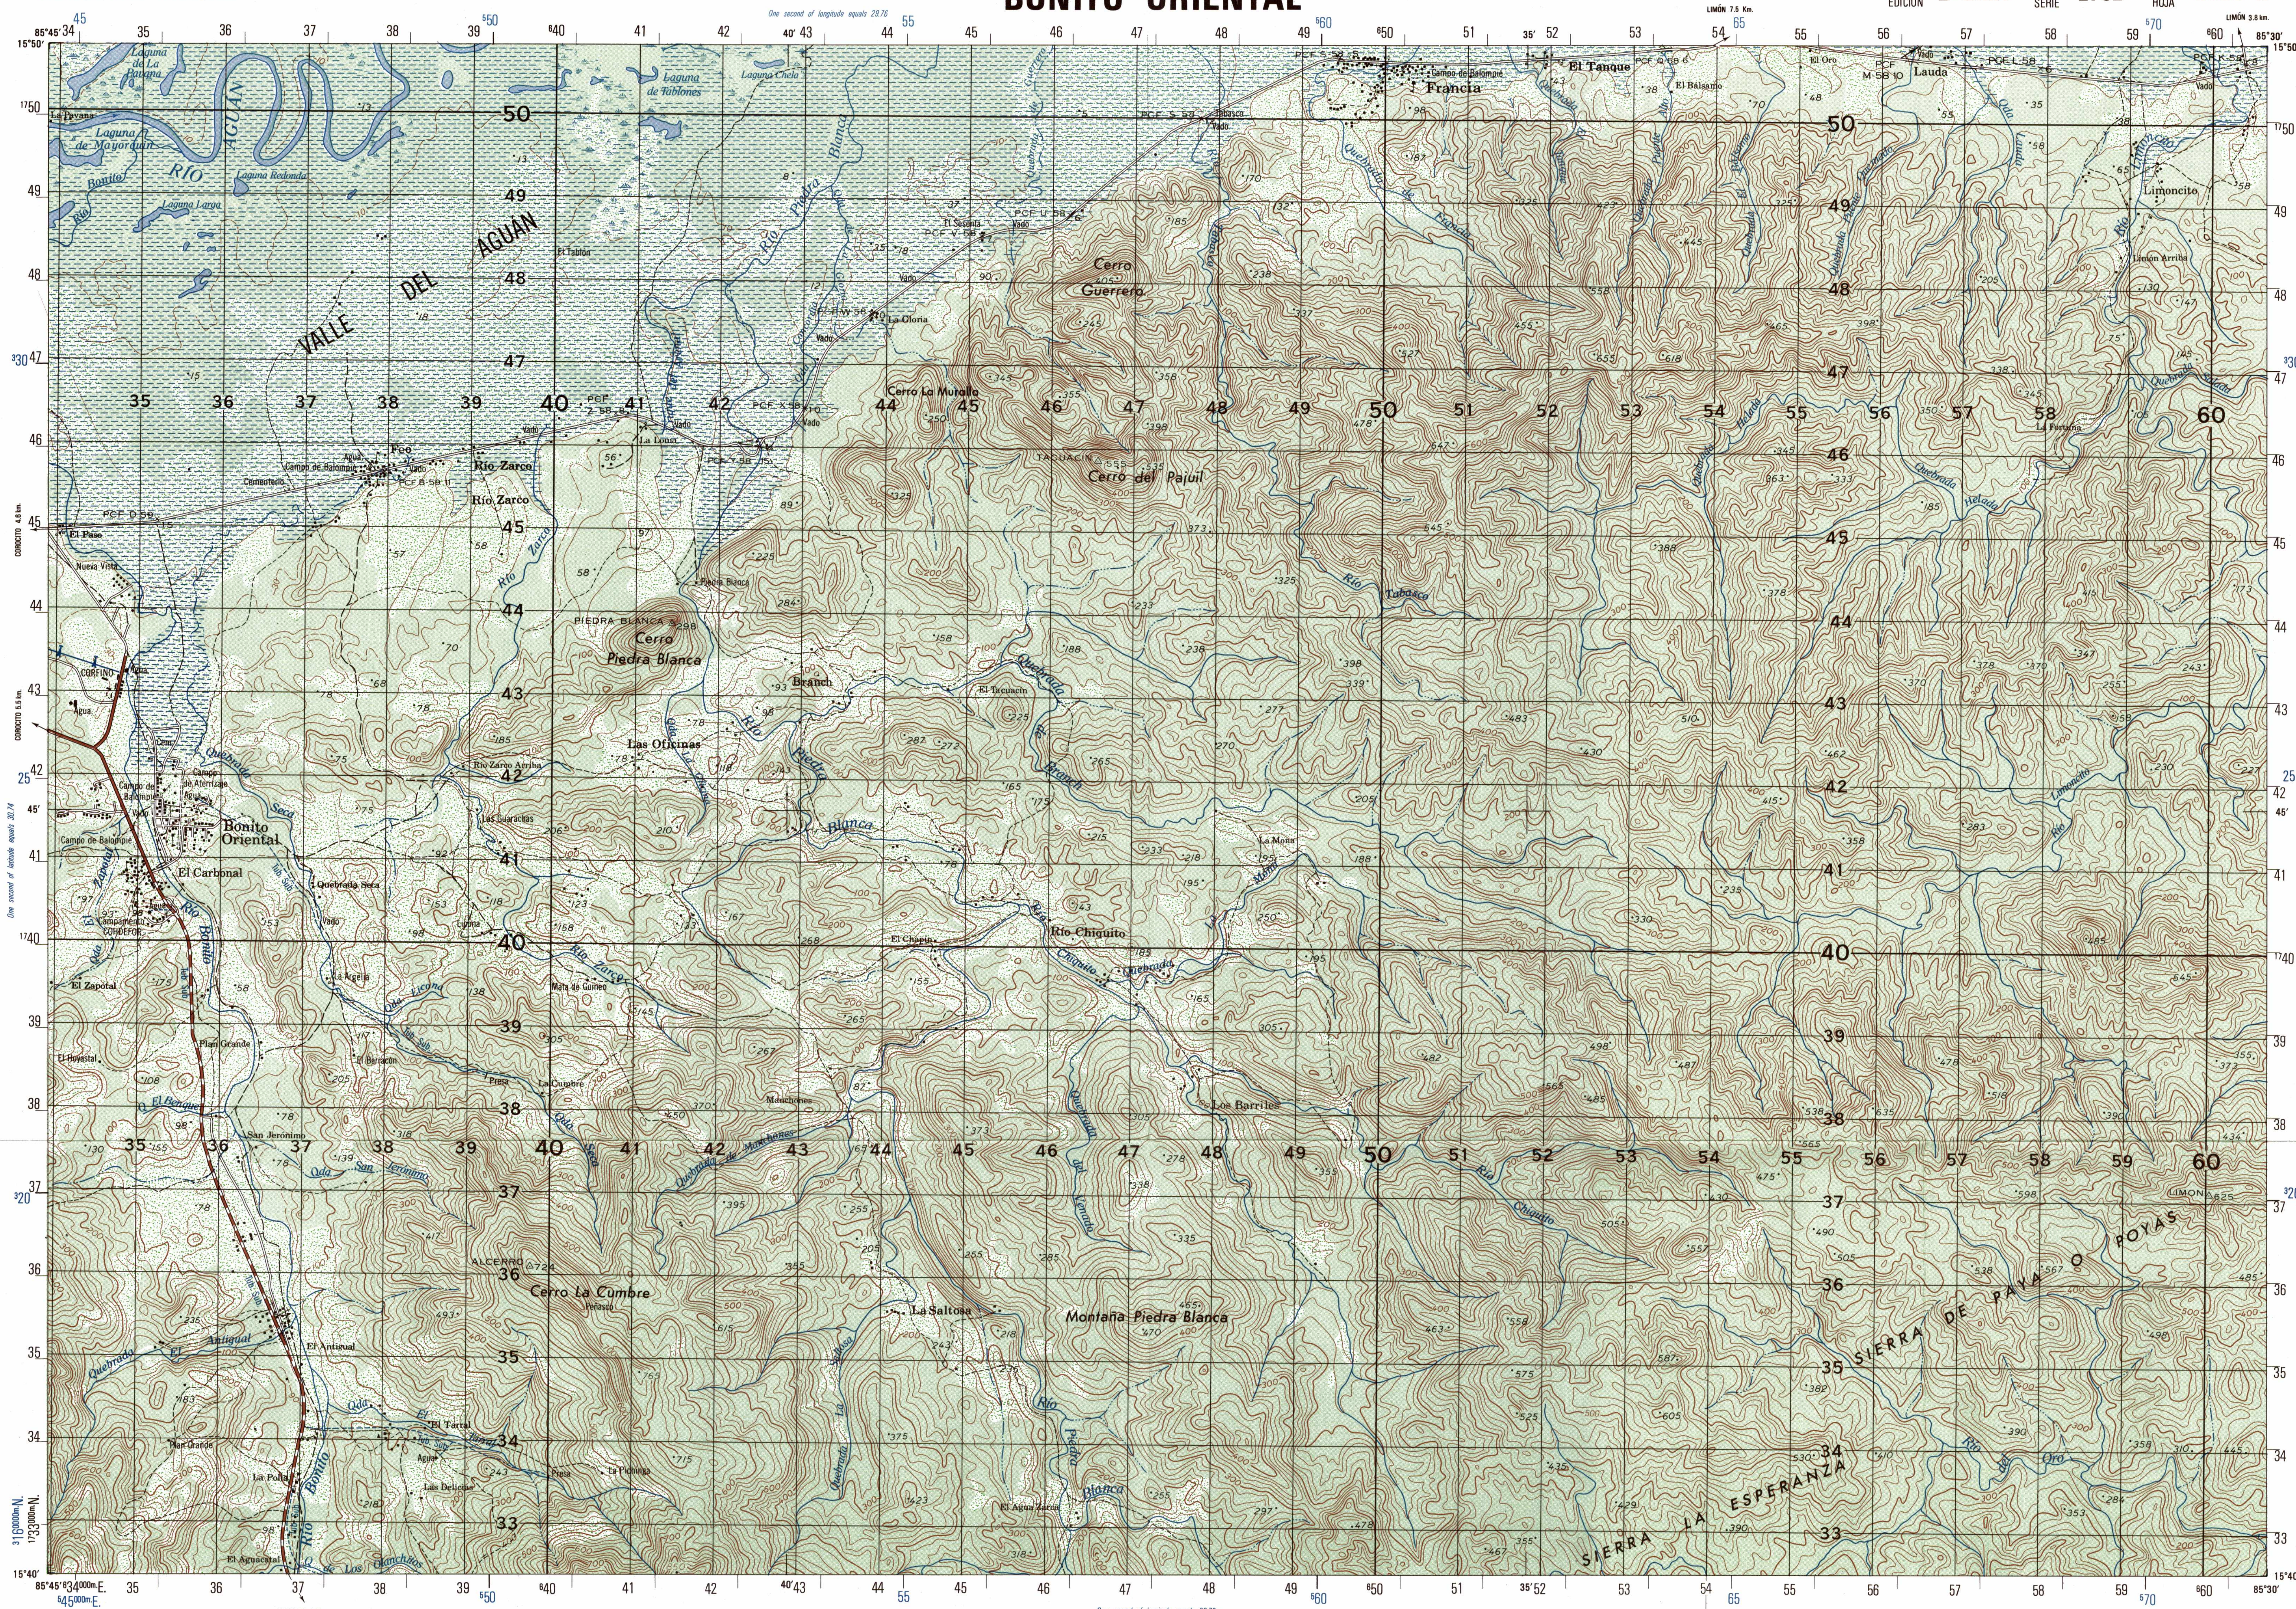

Prepared jointly by the Instituto Geografico Nacional (IGN) and the Defense Mapping Agency Hydrographic/Topographic Center.

Preparado colectivamente por el Instituto Geografico Nacional (IGN) y el Defense Mapping Agency Hydrographic/Topographic Center.

COMPILED IN 1986 FROM BEST AVAILABLE SOURCE MATERIALS
COMPILACIÓN CARTOGRÁFICA HECHA EN 1986 DE LAS MEJORES FUENTES DISPONIBLES.

LEGEND
SIGNOS CONVENCIONALES

ROADS		CAMINOS
Dual highway		Autopista
All weather, hard surface, two or more lanes wide	3 VÍAS	Para todo tiempo, carretera pavimentada, dos o más vías
All weather, loose or light surface, two or more lanes wide	3 VÍAS	Para todo tiempo, carretera mejorada, dos o más vías
All weather, hard surface, one lane wide		Para todo tiempo, carretera pavimentada, una vía
All weather, loose or light surface one lane wide		Para todo tiempo, carretera mejorada, una vía
Fair or dry weather, loose surface		Camino transitable en verano
Cart track ; Trail		Camino de herradura; Rodera
Bridge		Puente
Route markers: National; Secondary	51 23	Señales de ruta Nacional; Secundaria

RAILROADS	Single / Una Vía	Multiple / Dos Vías	FERROCARRILES
Broad gauge 1.067m.(3.5′)			Vía ancha 1.067m.(3.5′)
Normal gauge .914m.(3′)			Vía normal .914m.(3′)
Narrow gauge			Vía estrecha
Station; Turntable			Estación; Plato giratoria

Built-up area		Área construida

BOUNDARIES	LÍMITES
International; Boundary marker	Internacional; Mojón limítrofe
First-order Administrative Division	Departamento

Building; Church; Native hut		Edificio; Iglesia; Choza, rancho
School; Cemetery		Escuela; Cementerio
Windmill, windpump; Watermill; Light, lighthouse		Molino de viento, aeromotor; Molino de agua; Luz, faro
Tank; Located object		Tanque; Punto conspicuo
Fence; Wall		Cerca; Muro
Power transmission line		Línea de transmisión
Telephone or telegraph line		Línea telefónica o línea telegráfica
Mine: Active; Abandoned		Mina: Activa; Abandonada
Horizontal control point; Bench mark	PCF × 24	Vértice geodésico Punto fijo
Spot elevations in meters: Checked; Unchecked	168 168	Cota en metros: Comprobadas; No comprobadas

STREAMS		RÍOS
Perennial		Perenne
Intermittent		Intermitente
Well; Spring; Intermittent lake		Pozo; Manantial; Lago intermitente
Land subject to inundation; Dry stream or wash		Terreno sujeto a inundación Río seco o aluvión
Dam: Masonry; Earthen		Presas: de fábrica; de tierra
Levee		Dique
Woods, brushwood; Scrub	🟩	Arboleda; Matorral
Sand; Lava	None None	Arena; Lava
Orchards; Coffee	None None	Huerta; Cafetal
Rice; Salt evaporator	None	Arrozal; Salina
Marsh or swamp; Mangrove	None	Pantano; Manglar
Scattered trees	None	Árboles esparcidos

NOTES
NOTAS

ON THIS MAP A LANE IS GENERALLY CONSIDERED AS BEING 8–12 FEET (2.5–3.6 METERS) WIDE.
EN ESTE MAPA UNA VÍA TIENE GENERALMENTE UNA ANCHURA DE 8–12 PIES (2.5–3.6 METROS).

NOT ALL TELEPHONE AND ELECTRIC SERVICE LINES ARE SHOWN.
NO SE MUESTRAN TODAS LAS LÍNEAS DE SERVICIO.

GLOSSARY
GLOSARIO

Agua	water
Campamento	campsite
Campo de Aterrizaje	airfield
Campo de Balompié	soccer field
Cem	cemetery
Cerro	mountain
Crique	stream
Laguna	lagoon
Montaña	mountain
Peñasco	boulder
Quebrada, Qda., Q.	stream
Río	stream
Sierra	mountain range
Tub. Sub.	underground pipeline
Vado	ford
Valle	valley

USERS SHOULD REFER CORRECTIONS, ADDITIONS, AND COMMENTS TO THE NIMA CUSTOMER HELP DESK: 1-800-455-0899; COMMERCIAL 314-260-5032; DSN 490-5032; OR WRITE TO:
DIRECTOR, NATIONAL IMAGERY AND MAPPING AGENCY,
ATTN.: COD, MAIL STOP P-37,
4600 SANGAMORE ROAD, BETHESDA, MD 20816-5003.

One second of longitude equals 29.78m

SCALE 1:50,000

Meters 1000 500 0 1 2 3 4 5 Kilometers
1 ½ 0 1 2 3 Statute Miles
1 ½ 0 1 2 3 Nautical Miles

ELEVATIONS IN METERS

CONTOUR INTERVAL 20 METERS
SUPPLEMENTARY CONTOURS 10 METERS

INTERVALO DE CURVAS 20 METROS
CURVAS SUPLEMENTARIAS 10 METROS

SPHEROID	CLARKE 1866
GRID	1,000 METER UTM ZONE 16 (BLACK NUMBERED LINES) 1,000 METER HONDURAS NORTH LAMBERT GRID (BLUE NUMBERED TICKS)
PROJECTION	TRANSVERSE MERCATOR
VERTICAL DATUM	MEAN SEA LEVEL
HORIZONTAL DATUM	NORTH AMERICAN 1927 DATUM
PRINTED BY	NIMA 4-99

ESFEROIDE	CLARKE 1866
CUADRÍCULA	TRANSVERSA DE MERCATOR A 1,000 METROS ZONA 16 (LÍNEAS NEGRAS NUMERADAS) LAMBERT A 1,000 METROS, CUADRÍCULA HONDURAS AL NORTE (CIFRAS AZULES NUMERADAS)
PROYECCIÓN	TRANSVERSA DE MERCATOR
DATUM VERTICAL	NIVEL MEDIO DEL MAR
DATUM HORIZONTAL	DATUM NORTEAMERICANO DE 1927
IMPRESO POR	NIMA 4-99

SAMPLE 1,000 METER GRID SQUARE
EJEMPLO DEL CUADRADO DE 1,000 METROS

100,000 M. SQUARE IDENTIFICATION
IDENTIFICACIÓN DE CUADRÍCULA DE 100,000 METROS

FN

GRID ZONE DESIGNATION
DESIGNACIÓN DE ZONA DE CUADRÍCULA

16P

100 METER REFERENCE

1. Read large numbers labeling the VERTICAL grid line left of point and estimate tenths (100 meters) from grid line to point. 12 3
2. Read large numbers labeling the HORIZONTAL grid line below point and estimate tenths (100 meters) from grid line to point. 45 6

Example: 123456

WHEN REPORTING ACROSS A 100,000 METER LINE, PREFIX THE 100,000 METER SQUARE IDENTIFICATION IN WHICH THE POINT LIES.

Example: FN123456

WHEN REPORTING OUTSIDE THE GRID ZONE DESIGNATION AREA, PREFIX THE GRID ZONE DESIGNATION.

Example: 16PFN123456

REFERENCIA DE 100 METROS

1. Léanse las cifras grandes correspondientes a la línea VERTICAL de la cuadrícula situada a la izquierda del punto y estimarse los décimos (100 metros) entre la línea mencionada y el punto. 12 3
2. Léanse las cifras grandes correspondientes a la línea HORIZONTAL de la cuadrícula situada debajo del punto y estimarse los décimos (100 metros) entre la línea mencionada y el punto. 45 6

Ejemplo: 123456

CUANDO SE HACE REFERENCIA A UN PUNTO AL OTRO LADO DE UNA LÍNEA DE 100,000 METROS, ANTEPÓNGASE A LA REFERENCIA ANTERIOR LA IDENTIFICACIÓN DE LA CUADRÍCULA DE 100,000 METROS, DENTRO DEL CUAL SE ENCUENTRA EL PUNTO.

Ejemplo: FN123456

CUANDO SE HACE REFERENCIA FUERA DEL ÁREA DE LA ZONA DESIGNADA DE CUADRÍCULA ANTEPÓNGASE A LA REFERENCIA ANTERIOR LA DESIGNACIÓN DE LA ZONA DE CUADRÍCULA.

Ejemplo: 16PFN123456

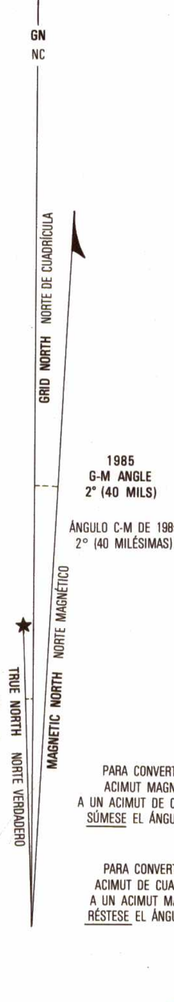

GN
NC
GRID NORTH NORTE DE CUADRÍCULA
MAGNETIC NORTH NORTE MAGNÉTICO
TRUE NORTH NORTE VERDADERO

1985
G-M ANGLE
2° (40 MILS)

ÁNGULO C-M DE 1985
2° (40 MILÉSIMAS)

GRID CONVERGENCE
0°22′ (6½ MILS)
FOR CENTER OF SHEET

CONVERGENCIA DE CUADRÍCULA
0°22′ (6½ MILÉSIMAS)
PARA EL CENTRO DE LA HOJA

TO CONVERT A MAGNETIC AZIMUTH TO A GRID AZIMUTH ADD G-M ANGLE

PARA CONVERTIR UN ACIMUT MAGNÉTICO A UN ACIMUT DE CUADRÍCULA SÚMESE EL ÁNGULO C-M

TO CONVERT A GRID AZIMUTH TO A MAGNETIC AZIMUTH SUBTRACT G-M ANGLE

PARA CONVERTIR UN ACIMUT DE CUADRÍCULA A UN ACIMUT MAGNÉTICO RÉSTESE EL ÁNGULO C-M

SLOPE GUIDE
GUÍA DE PENDIENTE

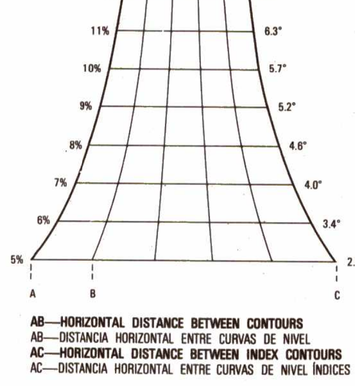

AB—HORIZONTAL DISTANCE BETWEEN CONTOURS
AB—DISTANCIA HORIZONTAL ENTRE CURVAS DE NIVEL
AC—HORIZONTAL DISTANCE BETWEEN INDEX CONTOURS
AC—DISTANCIA HORIZONTAL ENTRE CURVAS DE NIVEL ÍNDICES

THIS MAP IS RED-LIGHT READABLE

LIMITED DISTRIBUTION Distribution authorized to DoD, IAW 10 U.S.C. §§130 & 455. Release authorized to U.S. DoD contractors, IAW 48 C.F.R. §252.245-7000. Refer other requests to Headquarters, NIMA, ATTN: Release Officer, Stop P-25. Destroy as "For Official Use Only." "Removal of this caveat is prohibited."

CONVERSION GRAPH
GRÁFICO DE CONVERSIÓN

(1 meter = 3.28 feet)

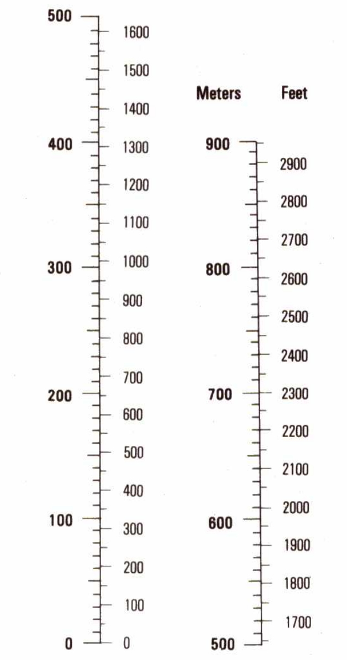

BOUNDARIES
LÍMITES

DEPARTAMENTO DE COLÓN

ADJOINING SHEETS
HOJAS ADYACENTES

3063 IV	3063 I	3163 IV
3063 III	3063 II	3163 III
3062 IV	3062 I	3162 IV

Sheet 3063 II falls within ND16-3, 1501, 1:250,000.

ELEVATION GUIDE GUÍA DE ELEVACIÓN

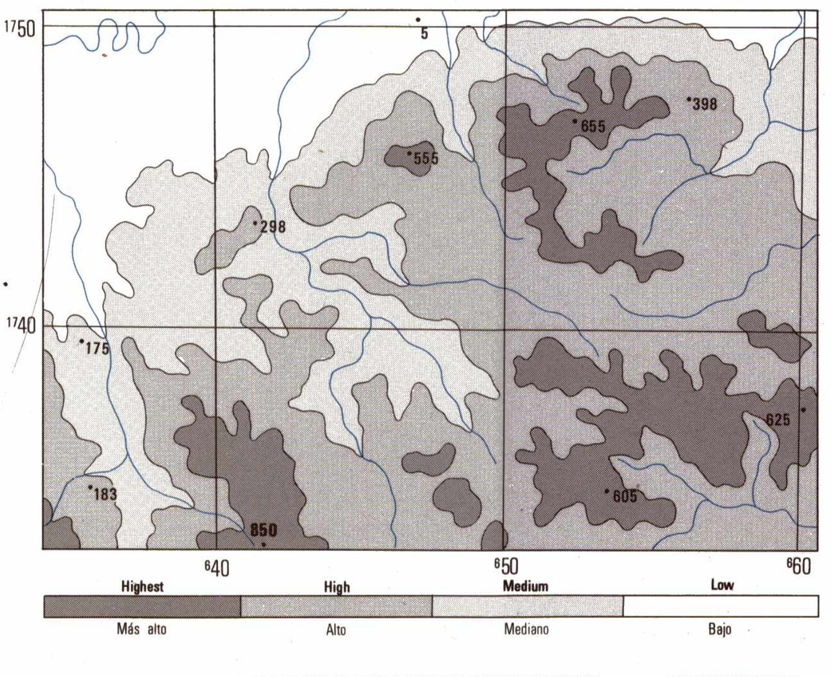

NSN 7643014052410
ED. NO. 002
NIMA REF. NO. E752X30632

BONITO ORIENTAL, HONDURAS 3063 II E752 EDITION 2–DMA