# HONDURAS 1:50,000

# EL CHICHICASTE

EDITION / EDICIÓN 1-DMA SERIES / SERIE E752 SHEET / HOJA 2958 III




Prepared and published by the Defense Mapping Agency Hydrographic/Topographic Center, Washington, D.C.

Scale 1:50,000

1000 500 0 1000 2000 3000 4000 5000 Meters
1000 500 0 1000 2000 3000 4000 5000 Yards
1 ½ 0 1 2 3 Statute Miles
1 ½ 0 1 2 3 Nautical Miles

CONTOUR INTERVAL 20 METERS
SUPPLEMENTARY CONTOURS 10 METERS

*INTERVALO DE CURVAS 20 METROS*
*CURVAS SUPLEMENTARIAS CADA 10 METROS*

## LEGEND — *SIGNOS CONVENCIONALES*

MAP INFORMATION AS OF 1979 — *INFORMACIÓN HASTA 1979*

On this map a lane is generally considered as being 8-12 feet (2.5-3.6 meters) in width
*EN ESTE MAPA UNA VÍA TIENE GENERALMENTE UNA ANCHURA DE 8-12 PIES (2.5 - 3.6 METROS)*

| ROADS | CAMINOS |
|---|---|
| Dual highway | Autopista |
| All weather, hard surface, two or more lanes wide (3 VÍAS) | Para todo tiempo, carretera pavimentada, dos o más vías |
| All weather, loose or light surface, two or more lanes wide (3 VÍAS) | Para todo tiempo, carretera mejorada, dos o más vías |
| All weather, hard surface, one lane wide | Para todo tiempo, carretera pavimentada, una vía |
| All weather, loose or light surface | Para todo tiempo, carretera mejorada |
| Fair or dry weather, loose surface | Camino transitable en verano |
| Cart track; Trail | Camino de herradura; Sendero |
| Bridge | Puente |
| Route markers: National; Secondary | Señales de ruta: Nacional; Secundaria |
| RAILROADS | FERROCARRILES |
| Normal gauge, single track (1.067m. (3.5')) | Vía normal, vía única |
| Narrow gauge, single track (.914m. (3')) | Vía estrecha, vía única |
| Built-up area | Área construida |
| BOUNDARIES | LÍMITES |
| International; Boundary marker | Internacional; Mojón limítrofe |
| First-order administrative division | Departamento |

| | |
|---|---|
| Power transmission line | Línea de transmisión |
| Fence; Wall | Cerca; Muro |
| Building; Church | Edificio; Iglesia |
| School; Cemetery | Escuela; Cementerio |
| Windmill, windpump; Water mill; Light, lighthouse | Molino de viento, aeromotor; Molino de agua; Luz, faro |
| Horizontal control point; Bench mark (BM×431) | Vértice geodésico; Punto fijo |
| Spot elevations in meters: Checked; Unchecked (×168 ×168) | Cota en metros: Comprobadas; No comprobadas |
| Sand; Lava | Arena; Lava |
| Woods, brushwoods; Scrub | Arboleda; Matorral |
| Permanent plantation; Bamboo | Plantación permenente; Bambú |
| Marsh or swamp; Mangrove | Pantano; Manglar |
| Nipa; Pine | Yolillo; Pino |
| Land subject to inundation; Dry stream or wash | Terreno sujeto a inundación; Río seco o aluvión |
| Well; Spring; Intermittent stream | Pozo; Manantial; Río intermitente |
| Intermittent lake; Navigable canal | Laguna intermitente; Canal navegable |
| Pier; Reef | Muelle; Arrecife |
| Dams: Masonry; Earthen | Presas: de fábrica; de tierra |


| | |
|---|---|
| SPHEROID | CLARKE 1866 |
| GRID | 1,000 METER UTM ZONE 16 (BLACK NUMBERED LINES) |
| | 1,000 METER LAMBERT, HONDURAS SOUTH ZONE (BLUE NUMBERED TICKS) |
| | 1,000 METER LAMBERT, NICARAGUA NORTH ZONE (BROWN NUMBERED TICKS) |
| PROJECTION | TRANSVERSE MERCATOR |
| VERTICAL DATUM | MEAN SEA LEVEL |
| HORIZONTAL DATUM | NORTH AMERICAN 1927 DATUM |
| CONTROL BY | NATIONAL GEOGRAPHIC INSTITUTE |

| | |
|---|---|
| *ESFEROIDE* | *CLARKE 1866* |
| *CUADRÍCULA* | *TRANSVERSA DE MERCATOR A 1,000 METROS, ZONA 16 (LÍNEAS NEGRAS NUMBERADAS)* |
| | *LAMBERT A 1,000 METROS, ZONA HONDURAS AL SUR (CIFRAS AZULES NUMERADAS)* |
| | *LAMBERT A 1,000 METROS, ZONA NICARAGUA AL NORTE (CIFRAS PARDAS NUMERADAS)* |
| *PROYECCION* | *TRANSVERSA DE MERCATOR* |
| *DATUM VERTICAL* | *NIVEL MEDIO DEL MAR* |
| *DATUM HORIZONTAL* | *DATUM NORTEAMERICANO DE 1927* |
| *CONTROL POR* | *INSTITUTO GEOGRAFICO NACIONAL* |

Reprinted by NIMA 02-99

USERS SHOULD REFER CORRECTIONS, ADDITIONS, AND COMMENTS TO THE NIMA CUSTOMER HELP DESK: 1-800-455-0899; COMMERCIAL 1-314-260-5032; DSN 490-5032; OR WRITE TO: ATTN: COD, MAIL STOP P-37, NATIONAL IMAGERY AND MAPPING AGENCY, 4600 SANGAMORE ROAD, BETHESDA MD 20816-5003.

| SAMPLE 1,000 METER GRID SQUARE / *EJEMPLO DEL CUADRADO DE 1,000 METROS* | 100 METER REFERENCE | *REFERENCIA DE 100 METROS* |
|---|---|---|
| 46 / × Sample point *Ejemplo* / 45 / 12 13 | 1. Read large numbers labeling the VERTICAL grid line left of point and estimate tenths (100 meters) from grid line to point. 12 3<br>2. Read large numbers labeling the HORIZONTAL grid line below point and estimate tenth (100 meters) from line to point. 45 6<br>Example: 123456 | *1. Léanse las cifras grandes correspondientes a la línea VERTICAL de la cuadrícula situada a la izquierda del punto y estímense los décimos (100 metros) entre la línea mencionada y el punto. 12 3*<br>*2. Léanse las cifras grandes correspondientes a la línea HORIZONTAL de la cuadrícula situada debajo del punto y estímense los décimos (100 metros) entre la línea mencionada y el punto 45 6*<br>*Ejemplo: 123456* |
| 100,000 M. SQUARE IDENTIFICATION / *IDENTIFICACIÓN DE CUADRÍCULA DE 100,000 M.* / EL | WHEN REPORTING ACROSS A 100,000 METER LINE, PREFIX THE 100,000 METER SQUARE IDENTIFICATION, IN WHICH THE POINT LIES.<br>Example: EL123456 | *CUANDO SE HACE REFERENCIA A UN PUNTO AL OTRO LADO DE UNA LÍNEA DE 100,000 METROS, ANTEPÓNGASE A LA REFERENCIA ANTERIOR LA IDENTIFICACIÓN DE LA CUADRÍCULA DE 100,000 METROS, DENTRO DEL CUAL SE ENCUENTRA EL PUNTO.*<br>*Ejemplo: EL123456* |
| GRID ZONE DESIGNATION / *DESIGNACIÓN DE ZONA DE CUADRÍCULA* / 16P | WHEN REPORTING OUTSIDE THE GRID ZONE DESIGNATION AREA, PREFIX THE GRID ZONE DESIGNATION.<br>Example: 16PEL123456 | *CUANDO SE HACE REFERENCIA FUERA DEL ÁREA DE LA ZONA DESIGNADA DE CUADRÍCULA ANTEPÓNGASE A LA REFERENCIA ANTERIOR LA DESIGNACIÓN DE LA ZONA DE CUADRÍCULA.*<br>*Ejemplo: 16PEL123456* |

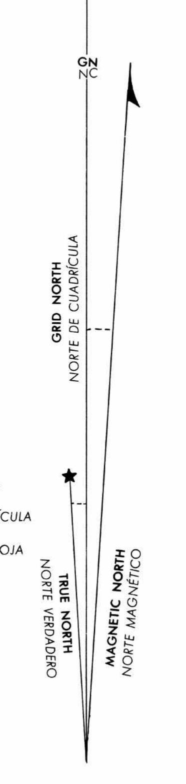


GRID CONVERGENCE
0°9' (3 MILS)
FOR CENTER OF SHEET

*CONVERGENCIA DE CUADRÍCULA*
*0°9' (3 MILÉSIMAS)*
*PARA EL CENTRO DE LA HOJA*

1980
G-M ANGLE
3½° (60 MILS)

*ÁNGULO C-M DE 1980*
*3½° (60 MILÉSIMAS)*


TO CONVERT A MAGNETIC AZIMUTH TO A GRID AZIMUTH ADD G-M ANGLE

*PARA CONVERTIR UN ACIMUT MAGNÉTICO A UN ACIMUT DE CUADRÍCULA SÚMESE EL ÁNGULO NC-M*

TO CONVERT A GRID AZIMUTH TO A MAGNETIC AZIMUTH SUBTRACT G-M ANGLE

*PARA CONVERTIR UN ACIMUT DE CUADRÍCULA A UN ACIMUT MAGNÉTICO RÉSTESE EL ÁNGULO NC-M*

## ELEVATION GUIDE
*GUÍA DE ELEVACÍON*

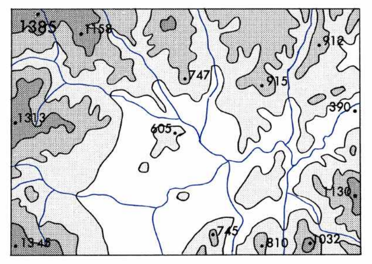


| | | |
|---|---|---|
| Highest | *Más Alto* |
| High | *Alto* |
| Medium | *Medio* |
| Low | *Bajo* |

## ADJOINING SHEETS
*HOJAS ADYACENTES*

| | | |
|---|---|---|
| 2858 I | 2958 IV | 2958 I |
| 2858 II | HONDURAS 2958 III | 2958 II |
| 2857 I | 2957 IV | E751 2957 I NICARAGUA |

## BOUNDARIES
*LÍMITES*

DEPARTAMENTO DE EL PARAÍSO

THE REPRESENTATION OF INTERNATIONAL BOUNDARIES IS NOT NECESSARILY AUTHORITATIVE.

**LIMITED DISTRIBUTION**
Distribution authorized to DoD, IAW 10 U.S.C. §§130 & 2796. Release authorized to U.S. DoD contractors IAW 48 C.F.R. §252.245-7000. Refer other requests to Headquarters, NIMA, ATTN: Release Officer, Stop P-25. Destroy as "For Official Use Only." Removal of this caveat is prohibited.

## GLOSSARY *GLOSARIO*

| | |
|---|---|
| Agua | water |
| Campo de Aterrizaje | landing field |
| Campo de Balompie | soccer field |
| Cem., Cementerio | cemetery |
| Cerro | hill |
| Cuchilla | mountain ridge |
| Depto., Departamento | first-order administrative division |
| Fca., Finca | farm |
| Hda., Hacienda | farm |
| Lin. Tel., Linea Telegráfica | telegraph line |
| Loma | hill |
| Montaña | mountain |
| Presa | dam |
| Q., Qda., Quebrada | stream |
| Rancho | farm |
| Represa | levee |
| Río | stream |
| Vado | ford |
| Valle | valley |
| Villa | settlement |

THIS MAP IS RED-LIGHT READABLE

NSN 7643014017984 ED. NO. 001
NIMA Ref No. E752X29583