


GLOSSARY
GLOSARIO

GLOSARIO	
Cem	cemetery
Cerro	mountain
Cordillera	mountain range
Fuente de Agua Termal	hot spring
Hacienda	estate
Lin. Tel	telegraph line
Loma	hill
Montaña	mountain
Cór., Quebrada	stream
Rio	stream
Vado	ford

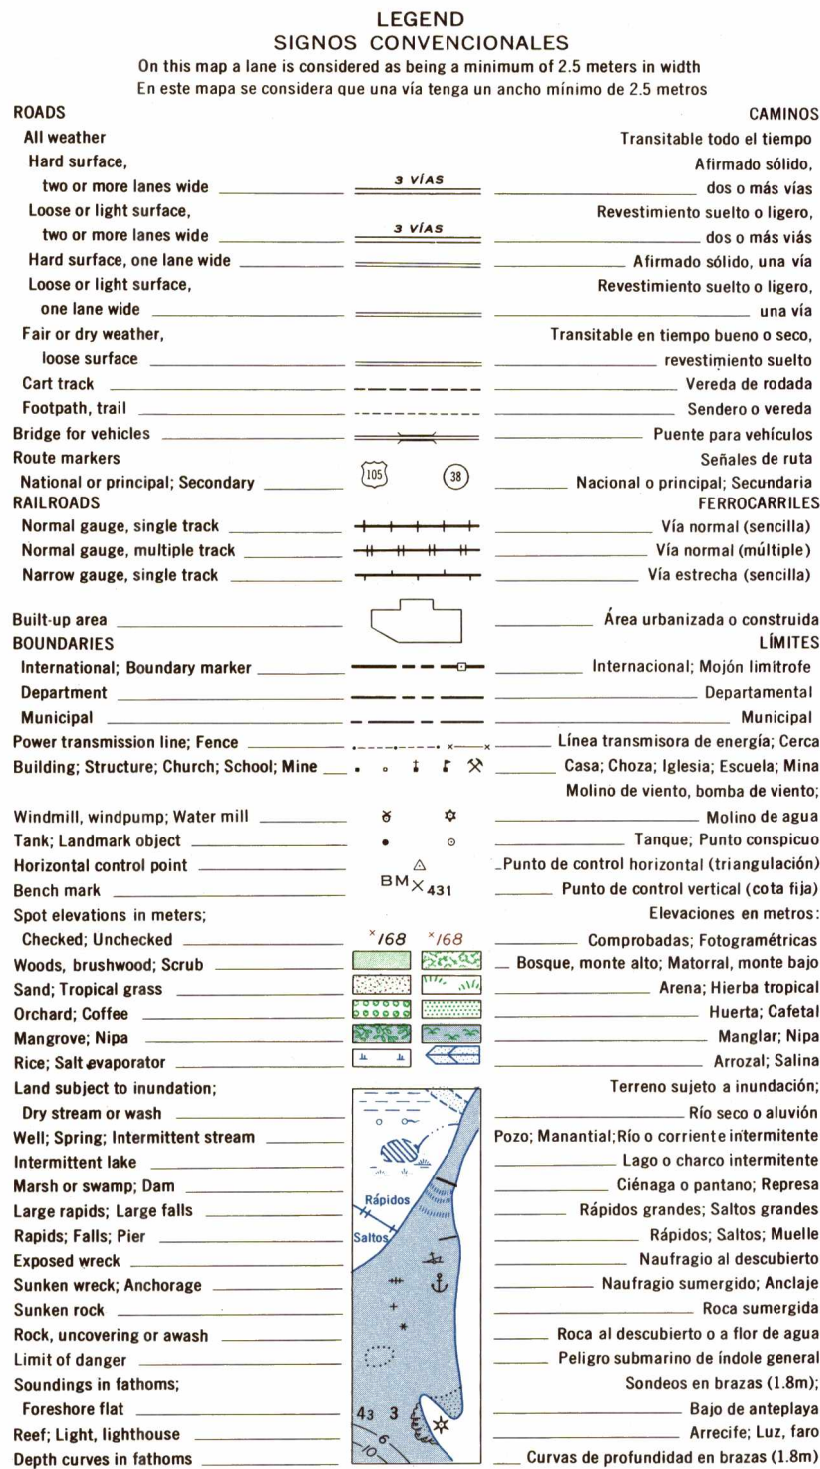

Prepared by the U.S. Army Topographic Command (SX), Washington, D.C., under the cooperative program of the Instituto Geográfico Nacional (IGN) of Honduras and the Inter-American Geodetic Survey (IAGS). Compiled in 1967 by photogrammetric methods. Aerial photography March 1960. Horizontal and vertical control by Dirección General de Cartografía and IAGS 1957. Field classification 1967. Map not field checked.

GRID CONVERGENCE
0°02' (1 MIL)
FOR CENTER OF SHEET

LA CONVERGENCIA DE LA CUADRA
0°02' (1 MILÉSIMA)
EN EL CENTRO DE LA HOJA

1970 G-M ANGLE
5° (90 MILS)

ÁNGULO C-M DE 1970
5° (90 MILÉSIMAS)

TO CONVERT A
MAGNETIC AZIMUTH
TO A GRID AZIMUTH
ADD G-M ANGLE

PARA CONVERTIR UN
ACIMUT MAGNÉTICO A
UN ACIMUT DE CUADRÍCULA
SE SUMA EL ÁNGULO C-M

TO CONVERT A
GRID AZIMUTH TO A
MAGNETIC AZIMUTH
SUBTRACT G-M ANGLE

PARA CONVERTIR UN
ACIMUT DE CUADRÍCULA A
UN ACIMUT MAGNÉTICO
SE RESTA EL ÁNGULO C-M

Scale 1:50,000

The graphic scale bar is divided into three horizontal sections. The top section is labeled 'Statute Miles' and has markings for 1, 1/2, 0, 1, 2, and 3. The middle section is labeled 'Meters' and has markings for 1000, 500, 0, 1000, 2000, 3000, and 4000. The bottom section is labeled 'Nautical Miles' and has markings for 1, 1/2, 0, 1, 2, and 3. The scale is 1:50,000.

CONTOUR INTERVAL 20 METERS

CURVAS DE NIVEL CADA 20 METROS

VERTICAL DATUM: MEAN SEA LEVEL

TRANSVERSE MERCATOR PROJECTION
HORIZONTAL DATUM: 1927 NORTH AMERICAN DATUM

HYDROGRAPHIC DATUM: APPROXIMATE MEAN LOW WATER

BLACK NUMBERED LINES INDICATE THE 1,000 METER UNIVERSAL TRANSVERSE MERCATOR GRID, ZONE 16, CLARKE 1866 SPHEROID
LAS LINEAS NEGRAS NUMERADAS INDICAN EL CUADRICULADO DE MIL METROS DE LA PROYECCIÓN
UNIVERSAL TRANSVERSAL DE MERCATOR, ZONA 16, ESFEROIDE DE CLARKE DE 1866


ED TICKS INSIDE THE NEATLINE INDICATE THE 1,000 METER LAMBERT GRID, HONDURAS NO
ARCAS CASTAÑO NUMERADAS DENTRO DEL PROYECTO INDICAN EL CUADRICULADO DE MIL
METROS DE LA PROYECCIÓN LAMBERT, ZONA DE HONDURAS NORTE

USERS SHOULD REFER CORRECTIONS, ADDITIONS, AND COMMENTS TO THE NIMA CUSTOMER HELP DESK: 1-800-455-0899
COMMERCIAL 314-260-5032; DSN 490-5032; OR WRITE TO: DIRECTOR, NATIONAL IMAGERY AND MAPPING AGENCY,
ATTN: COD, MAIL STOP P-37, 4600 SANGAMORE ROAD, BETHESDA, MD 20816-5003

1-71 PRINTED BY THE U.S. ARMY TOPOGRAPHIC COMMAND

Reprinted by NIMA 5-01

INDEX TO BOUNDARIES

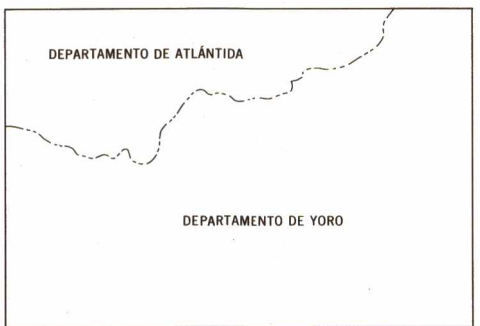

INDEX TO ADJOINING SHEETS

2762-IV	2762-I	2862-IV
2762-III	2762-II	2862-III
2761-IV	2761-I	2861-IV

Sheet 2762-III falls within ND 16-2, E503, 1:250,000

GRID ZONE DESIGNATION:
DESIGNACIÓN DE LA ZONA DE CUADRÍCULA

16P

100,000 M. SQUARE IDENTIFICATION
IDENTIFICACIÓN DEL CUADRADO DE
100,000 METROS

IDENTIFICACION DEL CUADRADO DE
100.000 METROS

DN

IGNORE the SMALLER figures of any grid number; these are for finding the full coordinates. Use ONLY the LARGER figures of the grid number;

cula; dichos números sólo sirven para conocer el valor completo de las coordenadas. Usense ÚNICAMENTE los números de tipo MÁS GRANDE, v.g.: 1696000m.
Example: Ejemplo:

TO GIVE A STANDARD REFERENCE ON THIS SHEET TO NEAREST 100 METERS	PARA DAR UNA REFERENCIA TIPO EN ESTA HOJA CON UNA APROXIMACIÓN DE 100 M.
---	---

SAMPLE POINT: PUNTO UTILIZADO COMO EJEMPLO: CEMENTERIO

1. Read letters identifying 100,000 meter square in which the point lies:	1. Léanse las letras que identifican el cuadrado de 100,000 m. dentro del cual se encuentra el punto.
2. Locate first VERTICAL grid line to LEFT of point and read LARGE figures labeling the line either in the top or bottom margin, or on the line itself:	2. Localícase la primera línea VERTICAL de la cual más próxima a la IZQUIERDA del punto los números en tipo GRANDE corresponden a la línea, ya sea en el margen superior o bien sobre la línea misma:

Estimate tenths from grid line to point:	Calcúlese los décimos del intervalo de x desde la línea mencionada al punto:
3. Locate first HORIZONTAL grid line BELOW point and read LARGE figures labeling the line either in the left or right margin, or on the line itself.	3. Localícese la primera línea HORIZONTAL <u>debajo</u> del punto y léanse las cifras <u>GRANDE</u> correspondientes a la misma que en el margen izquierdo o derecho o bien en la misma:

Estimate tenths from grid line to point:	Calcúlense los décimos (del intervalo de c...
SAMPLE REFERENCE:	REFERENCIA TIPO:
If reporting beyond 9°N-S or 18°E-W, prefix Grid Zone Designation, as:	Si se hace referencia a un punto más allá de 18° E-W, antepóngase la Designación de la Cuadrícula como sigue:

DN			
	83		
	2		
		99	

	DN832992
0 1	16PDN832992

JIMÍA, HONDURAS



NSN 7643014052846

NIMA REF. NO.



ED. NO. 001

E752X27622