SANTA BÁRBARA

EDITION 2–DMA EDICIÓN · SERIES E752 SERIE · SHEET 2560 I HOJA

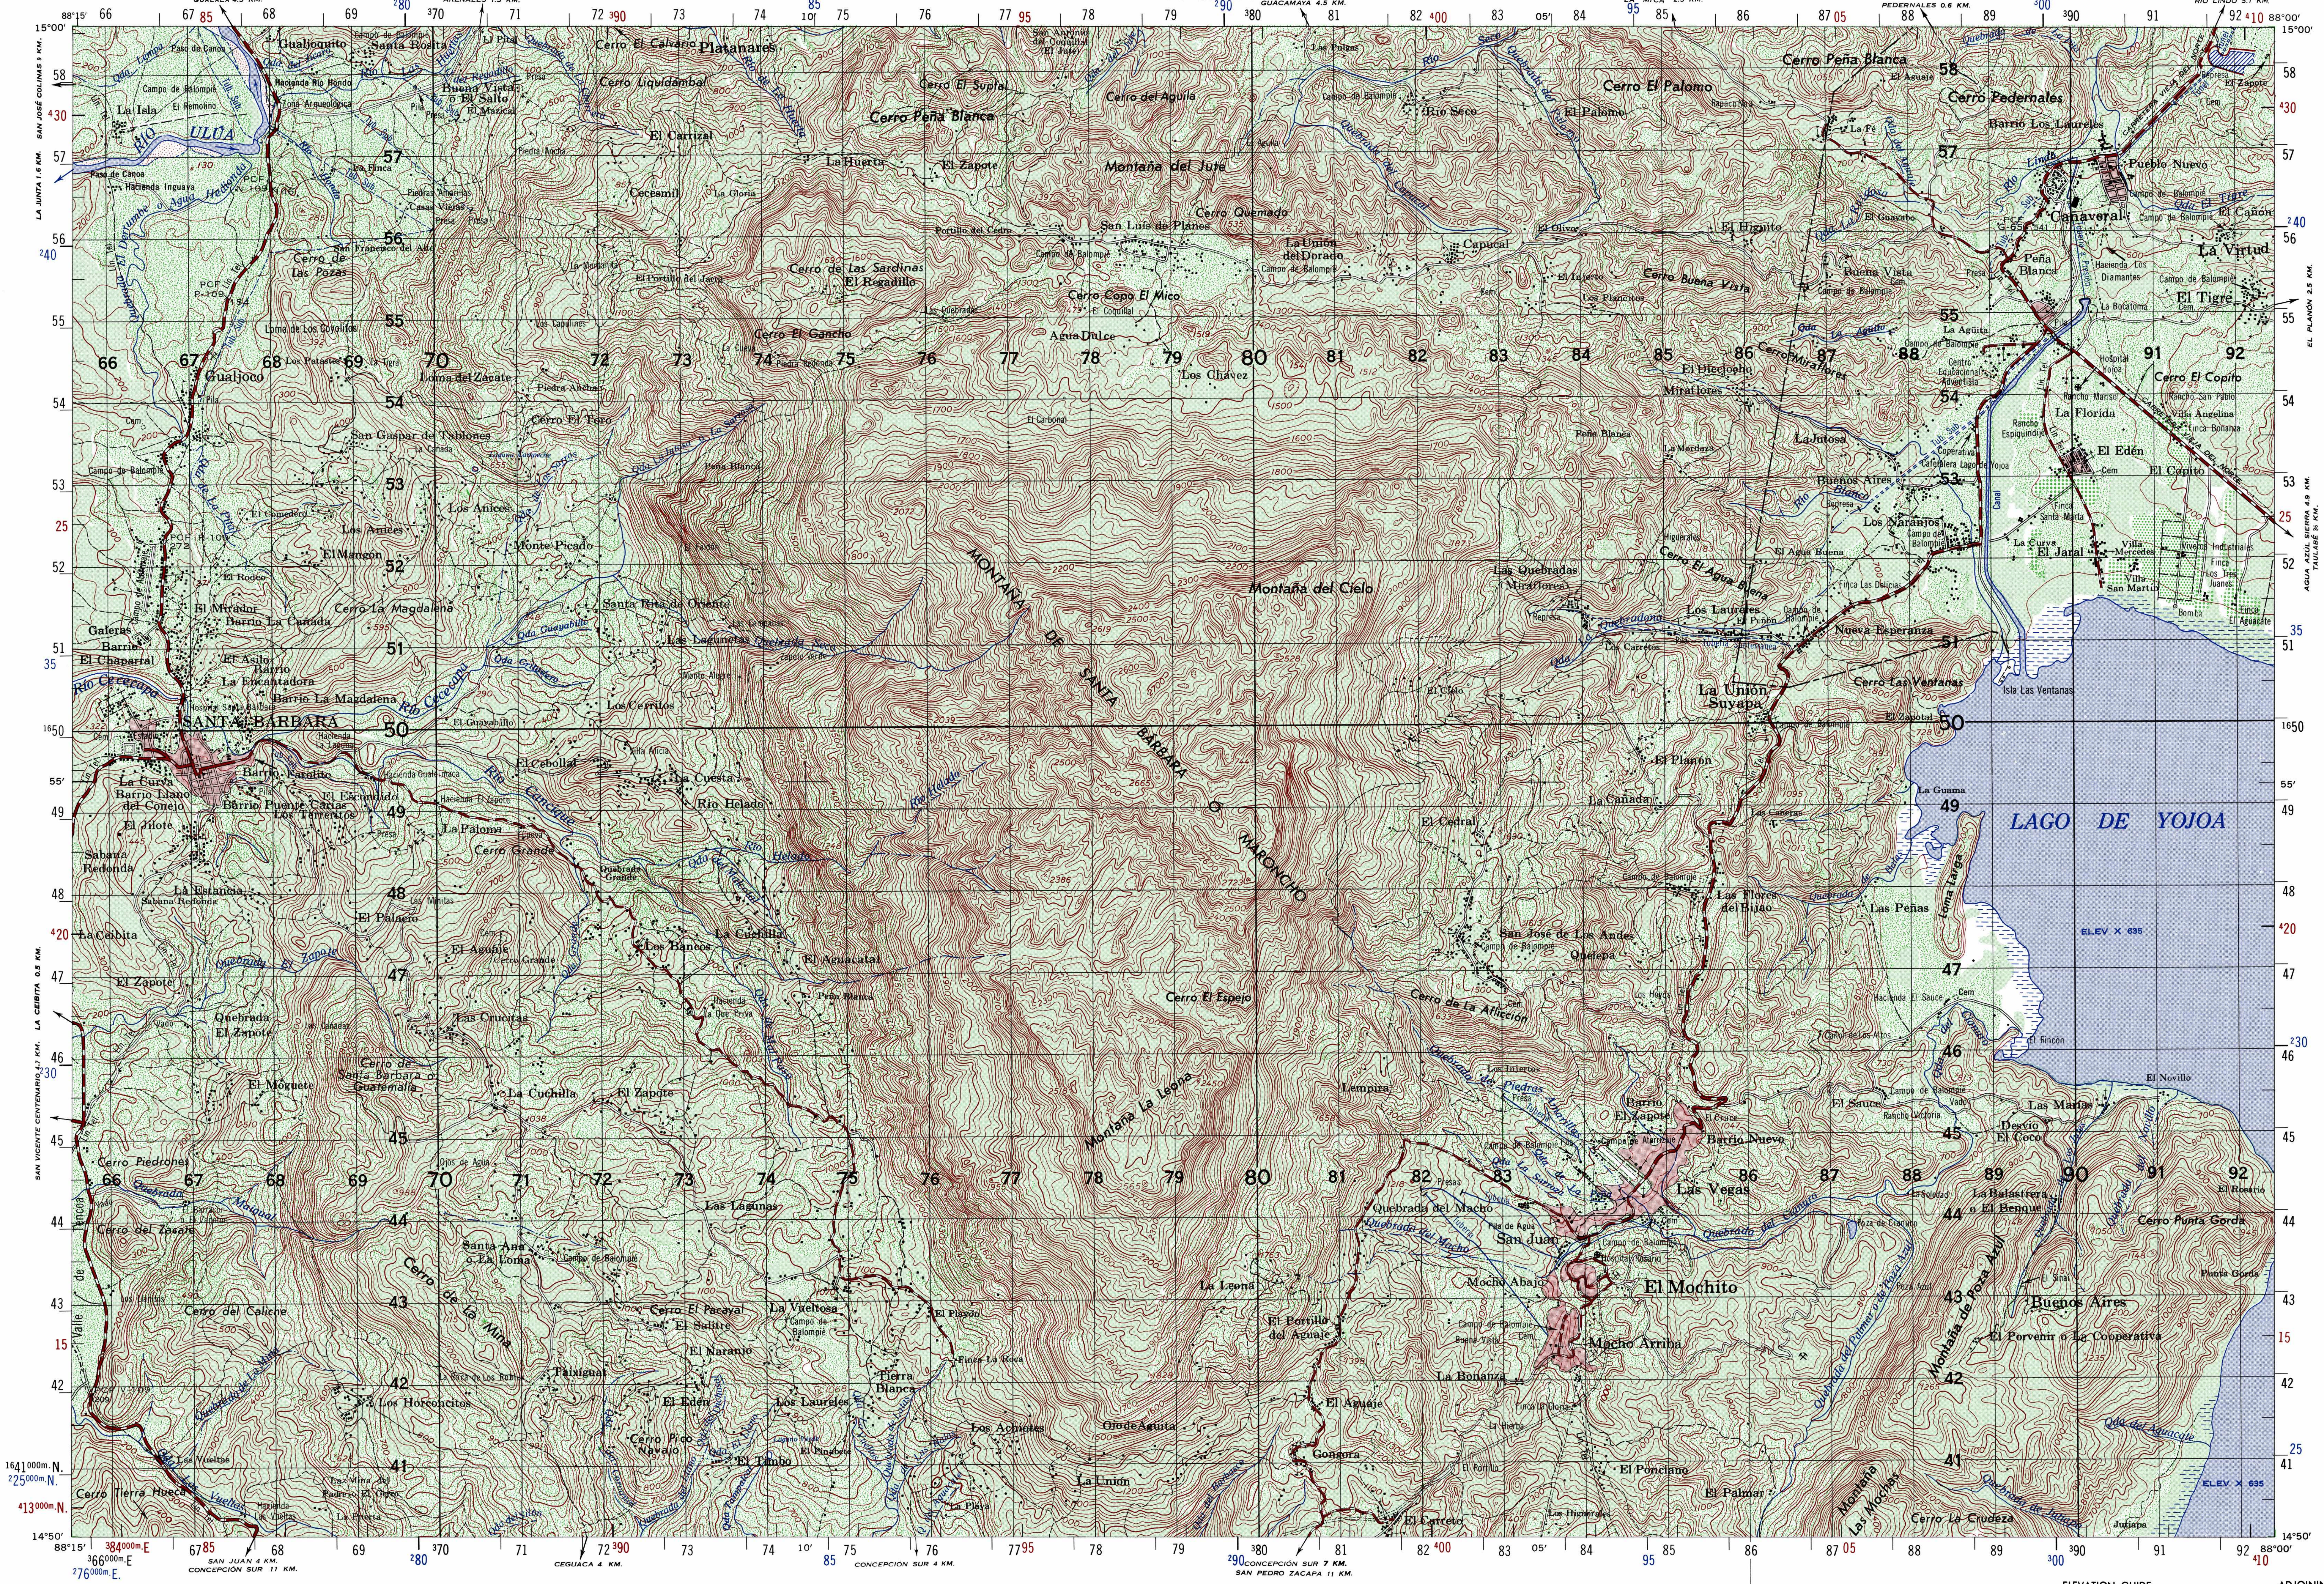

Prepared and published by the Defense Mapping Agency
Hydrographic/Topographic Center, Washington, D.C.

Scale 1:50,000

1000 500 0 1000 2000 3000 4000 5000 Meters
1000 500 0 1000 2000 3000 4000 5000 Yards
1 ½ 0 1 2 3 Statute Miles
1 ½ 0 1 2 3 Nautical Miles

CONTOUR INTERVAL 20 METERS — *INTERVALO DE CURVAS 20 METROS*

SPHEROID .... CLARKE 1866
GRID .... 1,000 METER UTM ZONE 16 (BLACK NUMBERED LINES)
1,000 METER LAMBERT, HONDURAS NORTH ZONE (BLUE NUMBERED TICKS)
1,000 METER LAMBERT, HONDURAS SOUTH ZONE (RED BROWN NUMBERED TICKS)
PROJECTION .... TRANSVERSE MERCATOR
VERTICAL DATUM .... MEAN SEA LEVEL
HORIZONTAL DATUM .... NORTH AMERICAN 1927 DATUM
CONTROL BY .... NATIONAL GEOGRAPHIC INSTITUTE

ESFEROIDE .... CLARKE 1866
CUADRÍCULA .... TRANSVERSA DE MERCATOR A 1,000 METROS, ZONA 16 (LÍNEAS NEGRAS NUMERADAS)
LAMBERT A 1,000 METROS, HONDURAS AL NORTE (CIFRAS AZULES NUMERADAS)
LAMBERT A 1,000 METROS, ZONA HONDURAS AL SUR (CIFRAS ROJAS PARDAS NUMERADAS)
PROYECCION .... TRANSVERSA DE MERCATOR
DATUM VERTICAL .... NIVEL MEDIO DEL MAR
DATUM HORIZONTAL .... DATUM NORTEAMERICANO DE 1927
CONTROL POR .... INSTITUTO GEOGRAFICO NACIONAL

Reprinted by NIMA 12-98

LEGEND — *SIGNOS CONVENCIONALES*

MAP INFORMATION AS OF 1982 — *INFORMACIÓN HASTA 1982*

On this map a lane is generally considered as being 8-12 feet (2.5-3.6 meters) in width
EN ESTE MAPA UNA VÍA TIENE GENERALMENTE UNA ANCHURA DE 8-12 PIES (2.5 - 3.6 METROS)

ROADS	CAMINOS
Dual highway	Autopista
All weather, hard surface, two or more lanes wide (3 VÍAS)	Para todo tiempo, carretera pavimentada, dos o más vías
All weather, loose or light surface, two or more lanes wide (3 VÍAS)	Para todo tiempo, carretera mejorada, dos o más vías
All weather, hard surface, one lane wide	Para todo tiempo, carretera pavimentada, una vía
All weather, loose or light surface	Para todo tiempo, carretera mejorada
Fair or dry weather, loose surface	Camino transitable en verano
Cart track; Trail	Camino de herradura; Sendero
Bridge	Puente
Route markers National; Secondary	Señales de ruta Nacional; Secundaria
RAILROADS	FERROCARRILES
Normal gauge, single track (1.067m. (3.5′))	Vía normal, vía única
Narrow gauge, single track (.914m. (3′))	Vía estrecha, vía única
Built-up area	Área construida
BOUNDARIES	LÍMITES
International; Boundary marker	Internacional; Mojón limítrofe
First-order administrative division	Departamento

Power transmission line	Línea de transmisión
Fence; Wall	Cerca; Muro
Building; Church	Edificio; Iglesia
School; Cemetery	Escuela; Cementerio
Windmill, windpump; Water mill; Light, lighthouse	Molino de viento, aeromotor; Molino de agua; Luz, faro
Horizontal control point; Bench mark (BM×431)	Vértice geodésico; Punto fijo
Spot elevations in meters: Checked; Unchecked (×168 ×168)	Cota en metros: Comprobadas; No comprobadas
Sand; Lava	Arena; Lava
Woods, brushwoods; Scrub	Arboleda; Matorral
Permanent plantation; Bamboo	Plantación permenente; Bambú
Marsh or swamp; Mangrove	Pantano; Manglar
Nipa; Pine	Yolillo; Pino
Land subject to inundation;	Terreno sujeto a inundación;
Dry stream or wash	Río seco o aluvión
Well; Spring; Intermittent stream	Pozo; Manantial; Río intermitente
Intermittent lake; Navigable canal	Laguna intermitente; Canal navegable
Pier; Reef	Muelle; Arrecife
Dams: Masonry; Earthen	Presas: de fábrica; de tierra

SAMPLE 1,000 METER GRID SQUARE / *EJEMPLO DEL CUADRADO DE 1,000 METROS*	100 METER REFERENCE	*REFERENCIA DE 100 METROS*
46 / 45; 12 / 13; × Sample point *Ejemplo*	1. Read large numbers labeling the VERTICAL grid line left of point and estimate tenths (100 meters) from grid line to point. 12 3 2. Read large numbers labeling the HORIZONTAL grid line below point and estimate tenth (100 meters) from line to point. 45 6 Example: 123456	*1. Léanse las cifras grandes correspondientes a la línea VERTICAL de la cuadrícula situada a la izquierda del punto y estímense los décimos (100 metros) entre la línea mencionada y el punto. 12 3* *2. Léanse las cifras grandes correspondientes a la línea HORIZONTAL de la cuadrícula situada debajo del punto y estímense los décimos (100 metros) entre la línea mencionada y el punto 45 6* *Ejemplo: 123456*
100,000 M. SQUARE IDENTIFICATION / *IDENTIFICACIÓN DE CUADRÍCULA DE 100,000 M.* CM	WHEN REPORTING ACROSS A 100,000 METER LINE, PREFIX THE 100,000 METER SQUARE IDENTIFICATION, IN WHICH THE POINT LIES. Example: CM123456	*CUANDO SE HACE REFERENCIA A UN PUNTO AL OTRO LADO DE UNA LÍNEA DE 100,000 METROS, ANTEPÓNGASE A LA REFERENCIA ANTERIOR LA IDENTIFICACIÓN DE LA CUADRÍCULA DE 100,000 METROS, DENTRO DEL CUAL SE ENCUENTRA EL PUNTO.* *Ejemplo: CM123456*
GRID ZONE DESIGNATION / *DESIGNACIÓN DE ZONA DE CUADRÍCULA* 16P	WHEN REPORTING OUTSIDE THE GRID ZONE DESIGNATION AREA, PREFIX THE GRID ZONE DESIGNATION. Example: 16PCM123456	*CUANDO SE HACE REFERENCIA FUERA DEL ÁREA DE LA ZONA DESIGNADA DE CUADRÍCULA ANTEPÓNGASE A LA REFERENCIA ANTERIOR LA DESIGNACIÓN DE LA ZONA DE CUADRÍCULA.* *Ejemplo: 16PCM123456*

GRID CONVERGENCE 0°17′ (5 MILS) FOR CENTER OF SHEET
CONVERGENCE DE CUADRÍCULA 0°17′ (5 MILÉSIMAS) PARA EL CENTRO DE LA HOJA

TRUE NORTH — *NORTE VERDADERO*
GRID NORTH — *NORTE DE CUADRÍCULA*
MAGNETIC NORTH — *NORTE MAGNÉTICO*

1985 G-M ANGLE 4° (70 MILS)
ANGULO C-M DE 1985 4° (70 MILÉSIMAS)

TO CONVERT A MAGNETIC AZIMUTH TO A GRID AZIMUTH ADD G-M ANGLE
PARA CONVERTIR UN ACIMUT MAGNÉTICO A UN ACIMUT DE CUADRÍCULA SÚMESE EL ÁNGULO NC-M

TO CONVERT A GRID AZIMUTH TO A MAGNETIC AZIMUTH SUBTRACT G-M ANGLE
PARA CONVERTIR UN ACIMUT DE CUADRÍCULA A UN ACIMUT MAGNÉTICO RÉSTESE EL ÁNGULO NC-M

ELEVATION GUIDE — *GUÍA DE ELEVACÍON*

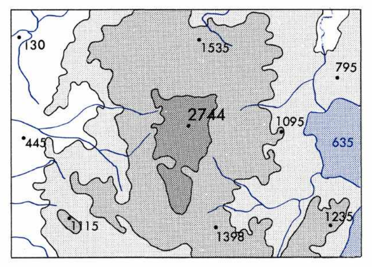

Highest	*Más alto*
High	*Alto*
Medium	*Medio*
Low	*Bajo*

ADJOINING SHEETS — *HOJAS ADYACENTES*

2561 III	2561 II	2661 III
2560 IV	2560 I	2660 IV
2560 III	2560 II	2660 III

BOUNDARIES — *LÍMITES*

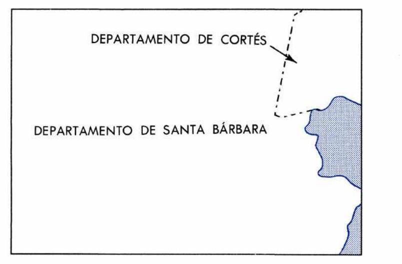

GLOSSARY — *GLOSARIO*

Bomba	pumping station
Campo de Aterrizaje	landing field
Campo de Balompie	soccer field
Canal	canal
Carretera	highway
Cementerio	cemetery
Cerro	mountain
Cueva	cave
Departamento	first-order administrative division
Elev., Elevación	elevation
Estadio	stadium
Finca	farm
Horno	kiln
Isla	island
Lago	lake
Laguna	lake
Lín. Tel., Línea Telefónica	telephone line
Loma	hill
Montaña	mountain
Peña	cliff, hill
Pila	pillar
Poza	pond
Presa	dam
Q., Qda., Quebrada	stream
Rancho	farm
Río	stream
Tuberia a presión	pipeline under pressure
Tub. Sub., Tuberia Subterranea	underground pipeline
Tunel	tunnel
Vado	ford
Valle	valley
Viveros Industriales	industrial fishery
Zona Arqueológica	archeological site

THIS MAP IS RED–LIGHT READABLE

LIMITED DISTRIBUTION

Distribution authorized to DoD, IAW 10 U.S.C. §§130 & 2796. Release authorized to U.S. DoD contractors IAW 48 C.F.R. §252.245-7000. Refer other requests to Headquarters, NIMA, ATTN: Release Officer, Stop P-25. Destroy as "For Official Use Only." Removal of this caveat is prohibited.

USERS SHOULD REFER CORRECTIONS ADDITIONS AND COMMENTS TO THE NIMA CUSTOMER HELP DESK 1-800-455-0899 COMMERCIAL 1-314-260-1236 DSN 490-1236 OR WRITE TO ATTN COD MAIL STOP P-37 NATIONAL IMAGERY AND MAPPING AGENCY 4600 SANGAMORE ROAD BETHESDA MD 20816-5003

NSN 7643014017897 ED. NO. 002
NIMA Ref No. E752X25601