

HONDURAS 1:50,000

SUBIRANA

EDITION 3–NIMA EDICIÓN | SERIES E752 SERIE | SHEET 2761 IV HOJA

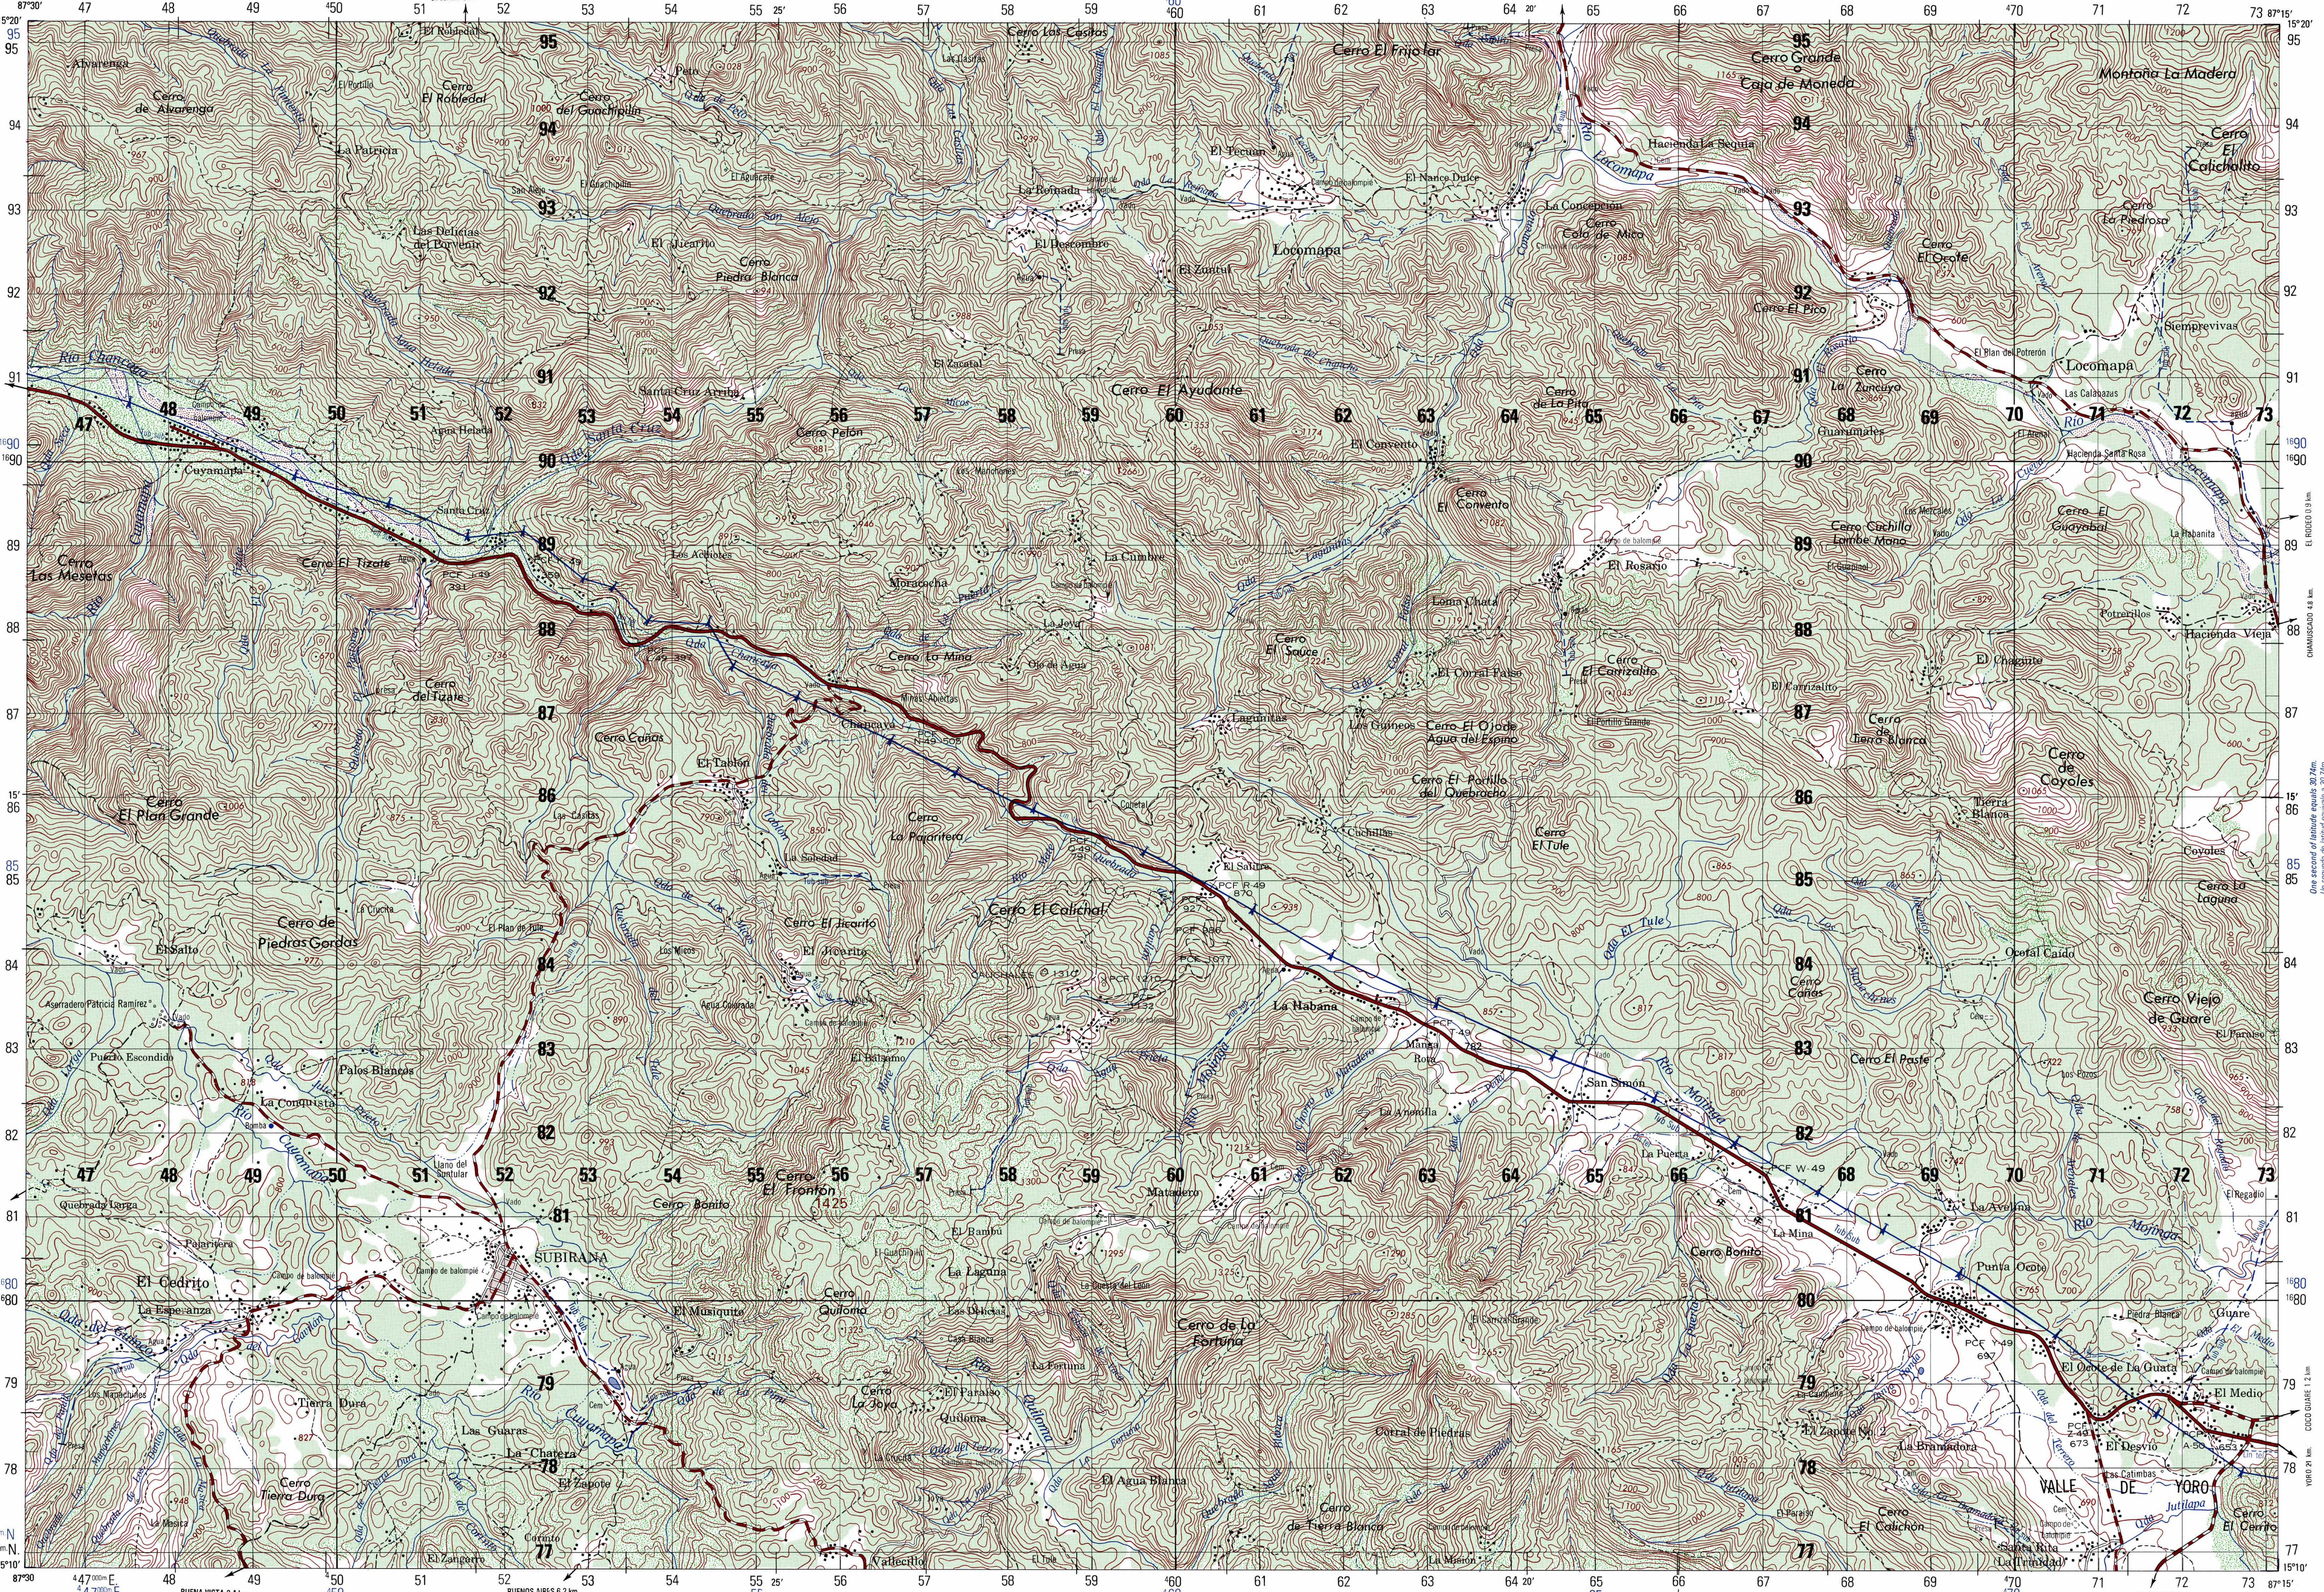

CONVERSION GRAPH
GRÁFICO DE CONVERSIÓN
(1 Meter = 3.28 Feet)
(1 Metro = 3.28 Pies)

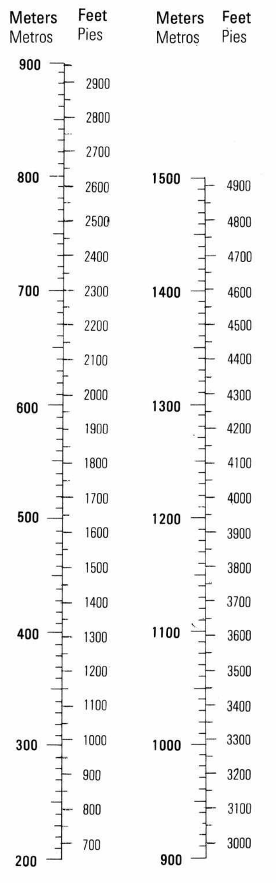

LIMITED DISTRIBUTION

Distribution authorized to DoD, IAW 10 U.S.C. §§130 & 455. Release authorized to U.S. DoD contractors, IAW 48 C.F.R. §252.245-7000. Refer other requests to Headquarters, NIMA, ATTN: Release Officer, Stop P-25. Destroy as "For Official Use Only." Removal of this caveat is prohibited.

DISTRIBUCIÓN LIMITADA

Distribución autorizada al Departamento de Defensa (DoD), IAW 10 U.S.C. §§130 & 455. Divulgación autorizada a contratistas del DoD de los E.E.U.U., IAW 48 C.F.R. §252.245-7000. Enviar otras solicitudes a Headquarters, NIMA, ATTN: Release Officer, Stop P-25. Destrúyase como "Para uso oficial solamente." Está prohibido remover este aviso.

Prepared by the Instituto Geográfico Nacional (IGN) Honduras with the collaboration of the National Imagery and Mapping Agency.

Preparado por el Instituto Geográfico Nacional (IGN) Honduras con la colaboración de la National Imagery and Mapping Agency.

NOTES NOTAS

CAUTION: NOT ALL TELEPHONE AND ELECTRIC SERVICE LINES ARE SHOWN.
ADVERTENCIA: NO TODAS LAS LÍNEAS TELEFONICAS Y DE DISTRIBUCIÓN ELÉCTRICA SE INDICAN

THE WIDTH OF A LANE ON THIS MAP IS CONSIDERED TO BE A MINIMUM OF 2.5 METERS.

UNA VIA EN ESTE MAPA SE CONSIDERA UN MINIMO DE 2.5 METROS DE ANCHO.

IN BUILT-UP AREAS ONLY THROUGH ROUTES ARE CLASSIFIED.

EN ÁREAS DESARROLLADAS SOLAMENTE SE CLASIFICAN LAS RUTAS TRONCALES.

Compiled by stereophotogrammetric methods from aerial photography taken in 1956. Updated by stereophotogrammetric methods in 1992 from aerial photography taken in 1977-78 and field classified in 1990.

Compilado por métodos estereofotogramétricos de fotografías aéreas tomadas en 1956. Actualizado por métodos estereofotogramétricos en 1992 con fotografías aéreas tomadas en 1977-78 y clasificadas en 1990.

SCALE 1:50,000 ESCALA 1:50,000

Metros Meters 1000 500 0 1 2 3 4 5 Kilometers Kilómetros
1 ½ 0 1 2 3 Statute Miles Millas Terrestres
1 ½ 0 1 2 3 Nautical Miles Millas Náuticas

ELEVATIONS IN METERS
ELEVACIONES EN METROS

CONTOUR INTERVAL 20 METERS — INTERVALO DE CURVAS 20 METROS

GRID; HORIZONTAL DATUM .... 1,000 METER UTM ZONE 16, GEODETIC REFERENCE SYSTEM 1980/WORLD GEODETIC SYSTEM 1984 ELLIPSOID; NORTH AMERICAN DATUM 1983/WORLD GEODETIC SYSTEM 1984 (BLACK NUMBERED LINES) 1,000 METER UTM ZONE 16, CLARKE 1866 ELLIPSOID; 1927 NORTH AMERICAN DATUM (BLUE NUMBERED TICKS)
PROJECTION .... TRANSVERSE MERCATOR
VERTICAL DATUM .... MEAN SEA LEVEL

CUADRÍCULA; DATUM HORIZONTAL .... 1,000 METROS UTM, ZONA 16 ELIPSOIDE 1980 DEL SISTEMA DE REFERENCIA GEODÉSICO/SISTÉMA GEODÉSICO MUNDIAL 1984; DATUM NORTEAMERICANO 1983/SISTEMA GEODÉSICO MUNDIAL 1984 (LÍNEAS NUMERADAS EN NEGRO) 1,000 METROS UTM ZONA 16, ELIPSOIDE DE CLARKE DE 1866; DATUM NORTEAMERICANO DE 1927 (TRAZOS NUMERADOS EN AZUL)
PROYECCIÓN .... TRANSVERSAL DE MERCATOR
DATUM VERTICAL .... NIVEL MEDIO DEL MAR

Reprinted by NIMA 3 - 99


SAMPLE 1,000 METER GRID SQUARE / EJEMPLO DEL CUADRADO DE 1,000 METROS	100 METER NAD 83/WGS 84 REFERENCE	REFERENCIA DE 100 METROS PARA NAD 83/WGS 84
Sample point / Ejemplo (84, 83, 58, 59)	1. Read large numbers labeling the VERTICAL grid line left of point and estimate tenths (100 meters) from grid line to point. 58 4 2. Read large numbers labeling the HORIZONTAL grid line below point and estimate tenths (100 meters) from grid line to point. 83 9 NAD 83 Example: 584839	1. Léanse las cifras grandes correspondientes a la línea VERTICAL de la cuadrícula situada a la izquierda del punto y estímense los décimos (100 metros) entre la línea mencionada y el punto. 58 4 2. Léanse las cifras grandes correspondientes a la línea HORIZONTAL de la cuadrícula situada debajo del punto y estímense los décimos (100 metros) entre la línea mencionada y el punto. 83 9 Ejemplo NAD 83: 584839
	100 METER NAD 27 REFERENCE 1. Estimated Easting value remains equal. 2. Subtract two tenths to estimated NAD 83 Northing: 453-2 = 451 NAD 27 Example: 584837	REFERENCIA DE 100 METROS PARA NAD 27 1. Valor estimado para el Este permanece igual. 2. Restar dos décimas al valor Norte estimado para NAD 83 453 -2 = 451 Ejemplo NAD 27: 584837
100,000 METER SQUARE IDENTIFICATION / IDENTIFICACIÓN DE CUADRÍCULA DE 100,000 METROS DB	WHEN REPORTING ACROSS A 100,000 METER LINE, PREFIX THE 100,000 METER SQUARE IDENTIFICATION IN WHICH THE POINT LIES. NAD 83 Example: 584839 NAD 27 Example: 584837	CUANDO SE HACE REFERENCIA A UN PUNTO AL OTRO LADO DE UNA LÍNEA DE 100,000 METROS, ANTEPÓNGASE LA REFERENCIA ANTERIOR LA IDENTIFICACIÓN DE LA CUADRÍCULA DE 100,000 METROS, DENTRO DEL CUAL SE ENCUENTRA EL PUNTO Ejemplo NAD 83: 584839 Ejemplo NAD 27: 584837
GRID ZONE DESIGNATION / DESIGNACIÓN DE ZONA DE CUADRÍCULA 16P	WHEN REPORTING OUTSIDE THE GRID ZONE DESIGNATION AREA, PREFIX THE GRID ZONE DESIGNATION. NAD 83 Example: 16P DB584839 NAD 27 Example: 16P DM584837	CUANDO SE HACE REFERENCIA FUERA DEL ÁREA DE LA ZONA DESIGNADA DE CUADRÍCULA ANTEPÓNGASE A LA REFERENCIA ANTERIOR LA DESIGNACIÓN DE LA ZONA DE CUADRÍCULA Ejemplo NAD 83: 16P DB584839 Ejemplo NAD 27: 16P DM584837

USERS SHOULD REFER CORRECTIONS, ADDITIONS, AND COMMENTS TO THE NIMA CUSTOMER HELP DESK: 1-800-455-0899; COMMERCIAL 1-314-260-5032; DSN 490-5032; OR WRITE TO: ATTN: COD, MAIL STOP P-37, NATIONAL IMAGERY AND MAPPING AGENCY, 4600 SANGAMORE ROAD, BETHESDA MD 20816-5003.


COORDINATE CONVERSION NAD 83/WGS 84 TO NAD 27
Grid: Subtract 7m.E.; Subtract 203 m.N.
Geographic: Add 0.2" Long.; Subtract 3.2" Lat.

CONVERSIÓN DE COORDENADAS NAD 83/WGS 84 A NAD 27
Cuadrícula: Restar 7m.E.; Restar 203 m.N.
Geográfico: Sumar 0.2" Long.; Restar 3.2" Lat.

BOUNDARIES LÍMITES

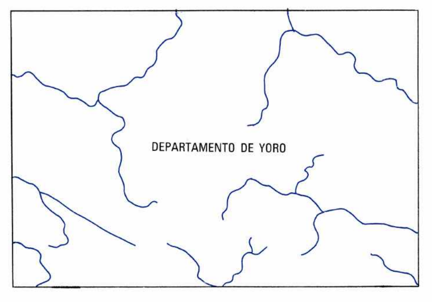


ADJOINING SHEETS HOJAS ADYACENTES

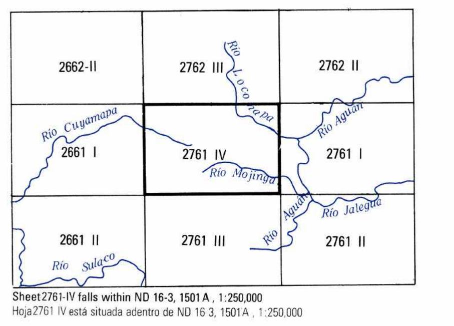

Sheet 2761-IV falls within ND 16-3, 1501 A, 1:250,000
Hoja 2761 IV está situada adentro de ND 16 3, 1501 A, 1:250,000

GRID COVERGENCE 0°06' (2 MILS) FOR CENTER OF SHEET

CONVERGENCIA DE CUADRÍCULA 0°06' (2 MILS) PARA EL CENTRO DE LA HOJA

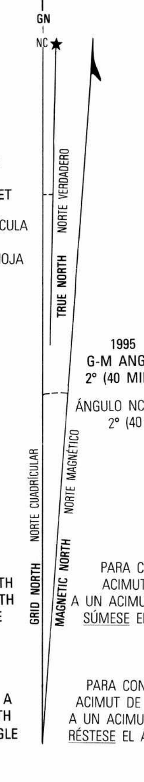

1995 G-M ANGLE 2° (40 MILS)

ÁNGULO NC-M DE 1995 2° (40 MILS)


TO CONVERT A MAGNETIC AZIMUTH TO A GRID AZIMUTH ADD G-M ANGLE

PARA CONVERTIR UN ACIMUT MAGNÉTICO A UN ACIMUT DE CUADRÍCULA SÚMESE EL ÁNGULO NC-M

TO CONVERT A GRID AZIMUTH TO A MAGNETIC AZIMUTH SUBTRACT G-M ANGLE


PARA CONVERTIR UN ACIMUT DE CUADRÍCULA A UN ACIMUT MAGNÉTICO RÉSTESE EL ÁNGULO NC-M

SLOPE GUIDE
GRADO DE PENDIENTE

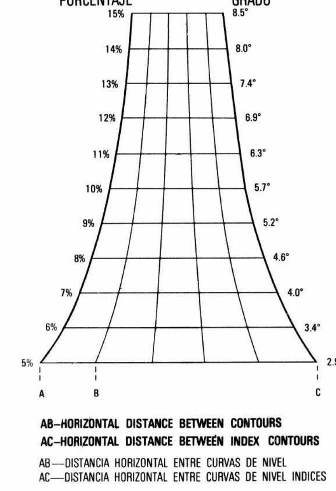

AB—HORIZONTAL DISTANCE BETWEEN CONTOURS
AC—HORIZONTAL DISTANCE BETWEEN INDEX CONTOURS
AB—DISTANCIA HORIZONTAL ENTRE CURVAS DE NIVEL
AC—DISTANCIA HORIZONTAL ENTRE CURVAS DE NIVEL INDICES

ELEVATION GUIDE GUÍA DE ELEVACIÓN

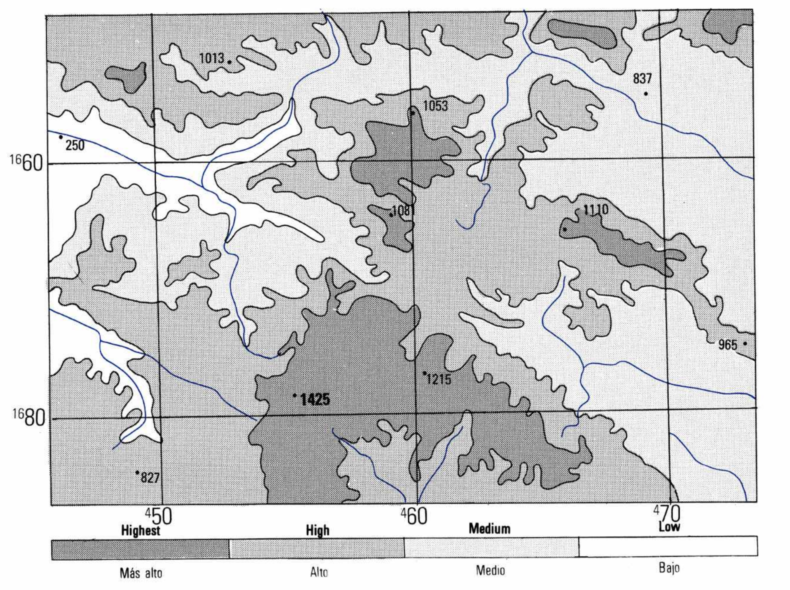

LEGEND CONVENCIONES

ROADS — CAMINOS
- Divided highway — Autopista con separador
- All weather, hard surface: — Transitable todo el tiempo, carretera pavimentada:
  - Two or more lanes wide — Dos o mas vías
  - One lane wide — Una vía
- All weather, loose surface: — Transitable todo el tiempo, revestimiento ligero:
  - Two or more lanes wide — Dos o mas vías
  - One lane wide — Una vía
- Fair or dry weather loose surface: — Transitable en tiempo seco, superficie ligera
- Track; Trail — Vereda de rodada; Sendero
- Bridge — Puente para vehículos
- Route markers: Primary; Secondary (46) (3) — Señal de ruta: Principal; Secundaria

RAILROADS — FERROCARRILES (Single Una vía; Multiple Dos vías)
- Normal gauge — Vía normal
- Narrow gauge — Vía estrecha
- Station — Estación

POPULATED PLACES — LUGARES POBLADOS
- Built-up area — Area urbanizada

BOUNDARIES — LIMITES
- International; Boundary marker — Internacional; Mojón limítrofe
- Administrative division: First-order: Departmental — División administrativa: Primer orden: Departamental

- Cemetery; Native hut — Cementerio; Choza, Rancho
- Building; Church; School — Edificio; Iglesia; Escuela
- Hospital; Located object — Hospital; Marca terrestre
- Windmill, windpump — Molino o bomba de viento
- Chimney; Tank — Chimenea; Tanque
- Mine: Active; Abandoned — Mina: Activa; Abandonada
- Horizontal control point — Punto de control horizontal
- Bench mark PCF X159 — Punto de control vertical
- Spot elevation in meters: Unchecked; Highest •250 •1425 — Punto de elevación en metros: No comprobado; Más alto
- Power transmission line — Línea transmisora de energía
- Telephone or telegraph line (Lin tel) — Línea telefónica o telegráfica
- Fence — Cerca
- Dam: Masonary; Earthen — Represa: Mampostería; Tierra
- Levee — Dique

DRAINAGE — DRENAJE
- Perennial — Perenne
- Intermittent; Disappearing — Intermitente; Desaparece
- Spring; Well — Manantial; Pozo
- Lake: Intermittent; Dry — Lago: Intermitente; Seco
- Rice; Salt evaporator (None / None) — Arrozal; Salinera
- Land subject to inundation (None) — Terreno sujeto a inundación
- Sand — Arena

VEGETATION — VEGETACIÓN
- Woodland, 3 meters or more in height — Bosque, 3 metros o mas de altura
- Scrub, Less than 3 meters high — Matorral, Menos de 3 metros de altura
- Plantation (None) — Plantación
- Marsh or swamp; Mangrove (None / None) — Ciénaga o Pantano; Manglar

GLOSSARY
GLOSARIO

- Agua .... water
- Aserradero .... sawmill
- Campo de balompié .... soccer field
- Cerro .... hill, mountain
- Bomba .... pump
- Hacienda, ... estate, farm, ranch
- Llano .... plain
- Montaña .... mountain
- Presa .... dam
- Quebrada, Qda. .... stream creek
- Río .... river
- Roca .... rock
- Tubería subterránea, Tub. sub. .... underground pipeline
- Vado .... ford
- Valle .... valley

THIS MAP IS RED-LIGHT READABLE
ESTE MAPA ES LEGIBLE BAJO LUZ ROJA

SUBIRANA, HONDURAS 2761 IV E752 EDITION 3–NIMA

NÚMERO DE SURTIDO NIMA E752X27614

NSN 7643014024678
NIMA REF. NO. E752X27614
ED. NO. 003