
HONDURAS 1:50,000

ZAPOTE

EDITION EDICIÓN 1–DMA SERIES SERIE E752 SHEET HOJA 3263 I

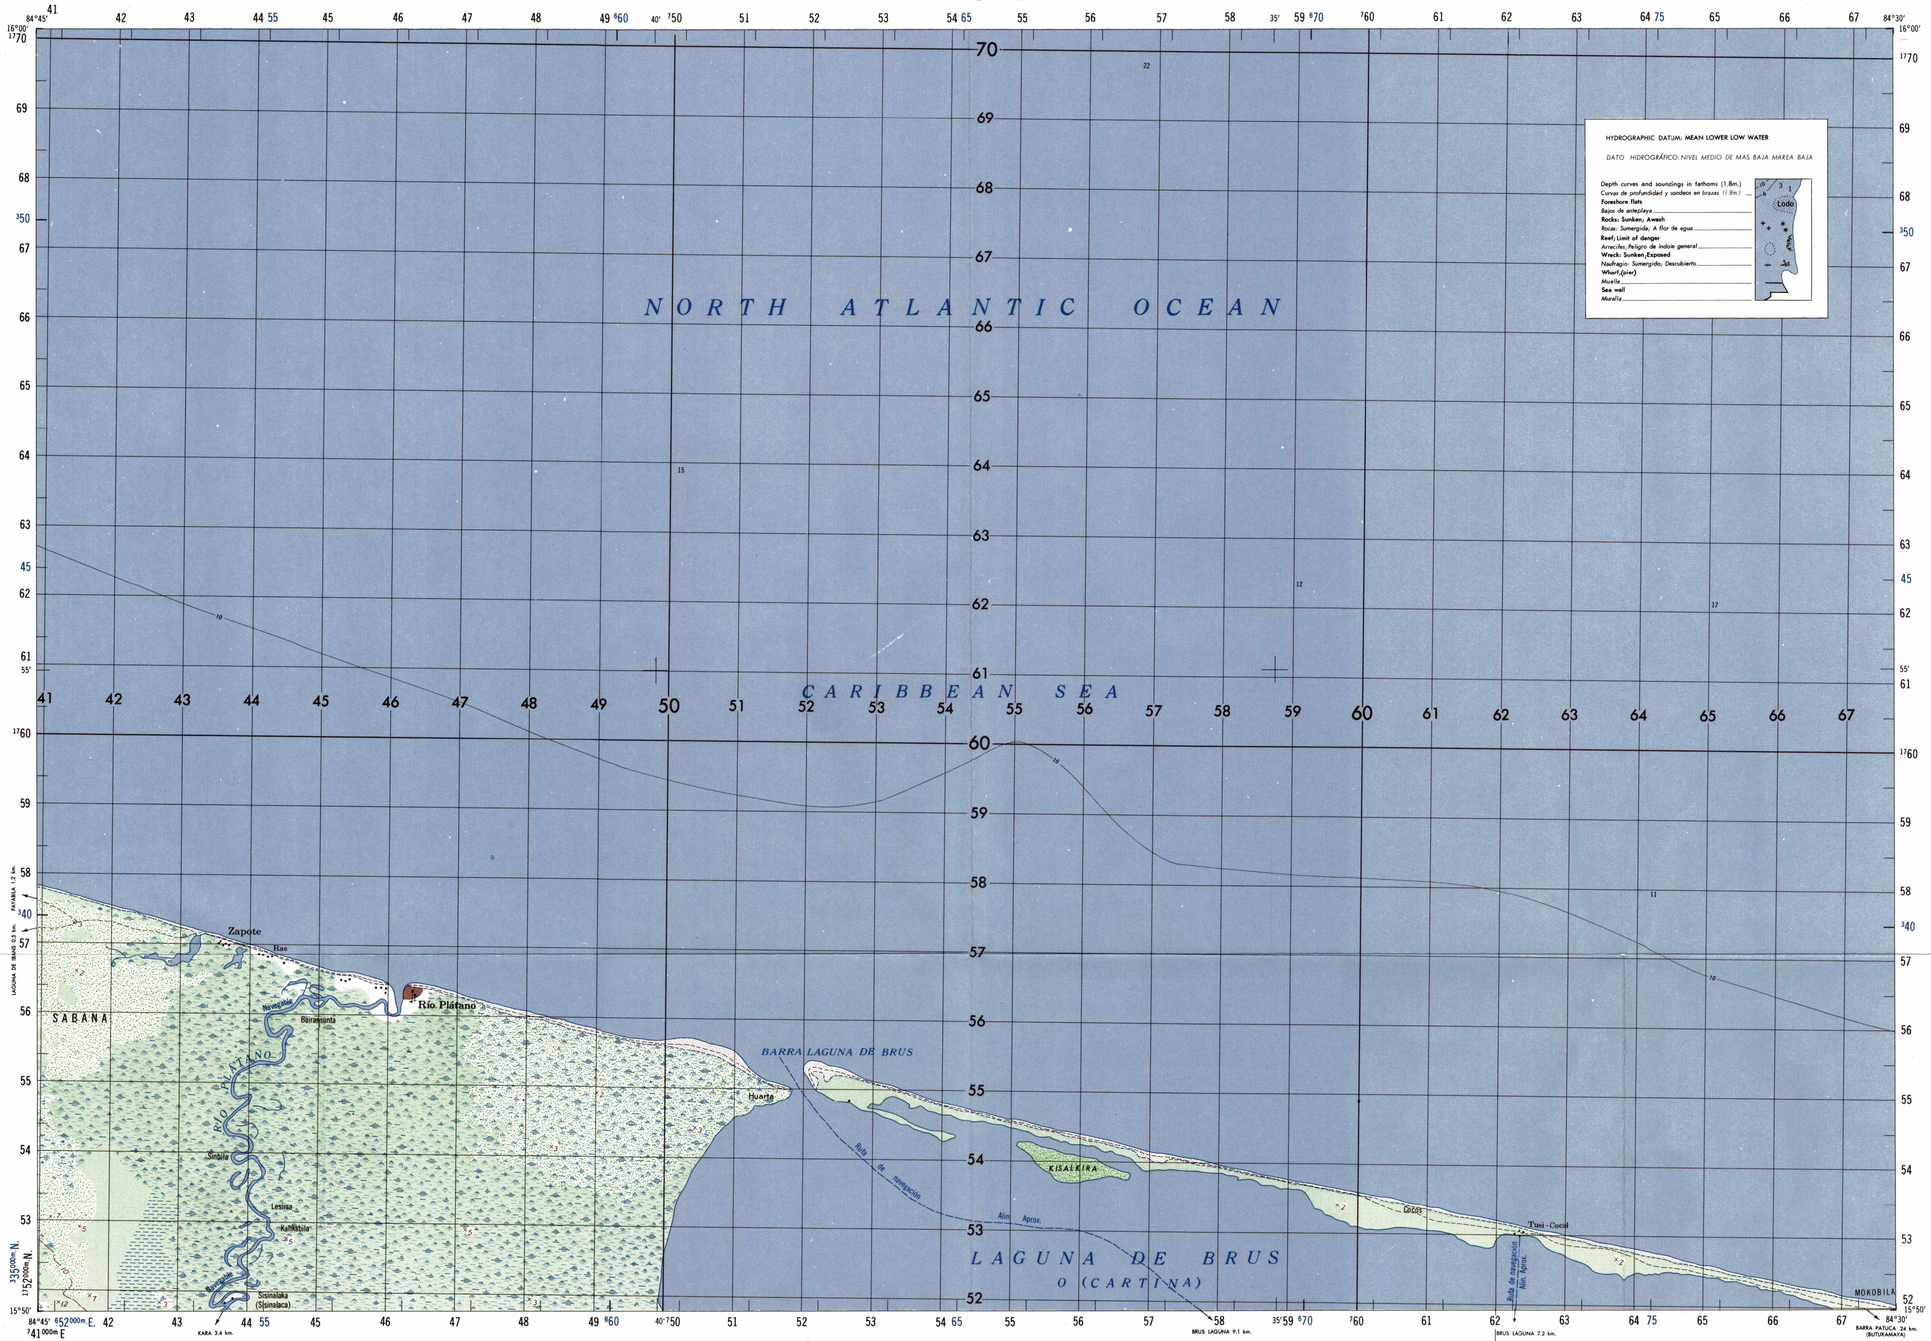

Prepared and published by the Defense Mapping Agency
Hydrographic/Topographic Center, Washington, D.C.

Scale 1:50,000

Meters 1000 500 0 1 2 3 4 5 Kilometers
1 ½ 0 1 2 3 Statute Miles
1 ½ 0 1 2 3 Nautical Miles

MAXIMUM ELEVATION 12 METERS
SUPPLEMENTARY CONTOURS 10 METERS

ELEVACIÓN MÁXIMA 12 METROS
CURVAS SUPLEMENTARIAS CADA 10 METROS

SPHEROID	CLARKE 1866
GRID	1,000 METER UTM ZONE 16 (BLACK NUMBERED LINES)
	1,000 METER, LAMBERT GRID, HONDURAS NORTH ZONE (BLUE NUMBERED TICKS)
PROJECTION	TRANSVERSE MERCATOR
VERTICAL DATUM	MEAN SEA LEVEL
HORIZONTAL DATUM	NORTH AMERICAN 1927 DATUM
CONTROL BY	NATIONAL GEOGRAPHIC INSTITUTE
Reprinted by NIMA 4-99	

ESFEROIDE	*CLARKE 1866*
CUADRÍCULA	*TRANSVERSA DE MERCATOR A 1,000 METROS, ZONA 16 LÍNEAS NEGRAS NUMERADAS*
	CUADRÍCULA LAMBERT A 1,000 METROS, ZONA HONDURAS AL NORTE CIFRAS AZULES NUMERADAS
PROYECCIÓN	*TRANSVERSA DE MERCATOR*
DATUM VERTICAL	*NIVEL MEDIO DEL MAR*
DATUM HORIZONTAL	*DATUM NORTEAMERICANO DE 1927*
CONTROL POR	*INSTITUTO GEOGRÁFICO NACIONAL*

USERS SHOULD REFER CORRECTIONS, ADDITIONS, AND COMMENTS TO THE NIMA CUSTOMER HELP DESK: 1-800-455-0899; COMMERCIAL 314-260-5032; DSN 490-5032; OR WRITE TO: DIRECTOR, NATIONAL IMAGERY AND MAPPING AGENCY, ATTN.: COD, MAIL STOP P-37, 4600 SANGAMORE ROAD, BETHESDA, MD 20816-5003.

SAMPLE 1,000 METER GRID SQUARE *EJEMPLO DEL CUADRADO DE 1,000 METROS*	100 METER REFERENCE	*REFERENCIA DE 100-METROS*
Sample point *Ejemplo* 46 45 12 13	1. Read large numbers lab=ling the VERTICAL grid line left of point and estimate tenths (100 meters) from grid line to point 12 3 2. Read large numbers labeling the HORIZONTAL grid line below point and estimate tenth (100 meters) from line to point 45 6	1. *Léanse las cifras grandes correspondientes a la línea VERTICAL de la cuadrícula situada a la izquierda del punto y estímense los décimos (100 metros) entre la línea mencionada y el punto.* 12 3 2. *Léanse las cifras grandes correspondientes a la línea HORIZONTAL de la cuadrícula situada debajo del punto y estímense los décimos (100 metros) entre la línea mencionada y el punto* 45 6
100,000 M. SQUARE IDENTIFICATION *IDENTIFICACIÓN DE CUADRÍCULA DE 100 000 M.* GN	Example: 123456 WHEN REPORTING ACROSS A 100,000 METER LINE, PREFIX THE 100,000 METER SQUARE IDENTIFICATION, IN WHICH THE POINT LIES. Example: GN123456	*Ejemplo: 123456* *CUANDO SE HACE REFERENCIA A UN PUNTO AL OTRO LADO DE UNA LÍNEA DE 100,000 METROS, ANTEPÓNGASE A LA REFERENCIA ANTERIOR LA IDENTIFICACIÓN DE LA CUADRÍCULA DE 100,000 METROS, DENTRO DEL CUAL SE ENCUENTRA EL PUNTO.* *Ejemplo: GN123456*
GRID ZONE DESIGNATION *DESIGNACIÓN DE ZONA DE CUADRÍCULA* 16P	WHEN REPORTING OUTSIDE THE GRID ZONE DESIGNATION AREA, PREFIX THE GRID ZONE DESIGNATION. Example: 16PGN123456	*CUANDO SE HACE REFERENCIA FUERA DEL ÁREA DE LA ZONA DESIGNADA DE CUADRÍCULA ANTEPÓNGASE A LA REFERENCIA ANTERIOR LA DESIGNACIÓN DE LA ZONA DE CUADRÍCULA.* *Ejemplo: 16PGN123456*

LEGEND
SIGNOS CONVENCIONALES

MAP INFORMATION AS OF 1968
INFORMACIÓN HASTA 1968

On this map a lane is generally considered as being 8-12 feet (2.5-3.6 meters) in width
EN ESTE MAPA UNA VÍA TIENE GENERALMENTE UNA ANCHURA DE 8-12 PIES (2.5 - 3.6 METROS)

ROADS	CAMINOS
Dual highway	Autopista
All weather, hard surface, two or more lanes wide (2 VÍAS)	Para todo tiempo, carretera pavimentada, dos o más vías
All weather, loose or light surface, two or more lanes wide (2 VÍAS)	Para todo tiempo, carretera mejorada, dos o más vías
All weather, hard surface, one lane wide	Para todo tiempo, carretera pavimentada, una vía
All weather, loose or light surface	Para todo tiempo, carretera mejorada
Fair or dry weather, loose surface	Camino transitable en verano
Cart track; trail	Camino de herradura; Huella
Bridge	Puente
Route markers	Señales de ruta
National; Secondary (1) (5)	Nacional; Secundaria
Railroad, normal gauge.	Ferrocarril, vía normal.
1.067m. (3'6")	1.067m. (3'6")
narrow gauge, 0.914m. (3')	vía estrecha, 0.914m. (3')
Built-up area	Area construida
BOUNDARIES	LIMITES
International; Boundary marker	Internacional; Mojón limítrofe
First-order administrative division	Departamento

Power transmission line	Línea de transmisión
Fence; Wall	Cerca; Muro
Building; Church; Tank	Edificio; Iglesia; Tanque
School; Cemetery	Escuela; Cementerio
Windmill, windpump; Water mill;	Molino de viento; aeromotor;
Light, lighthouse	Molino de agua; Luz, faro
Horizontal control point;	Vértice geodésico;
Bench mark (BM×431)	Punto fijo
Spot elevations in meters:	Cota en metros;
Checked; Unchecked (*160 *168)	Comprobadas; No comprobadas
Sand; Lava	Arena; Lava
Woods, brushwoods; Scrub	Arboleda; Matorral
Permanent plantation; Temporary	Plantación permanente; temporal
Marsh or swamp; Mangrove	Pantano; Manglar
Rice; Salt evaporator	Arrozal; Salina
Land subject to inundation;	Terreno sujeto a inundación;
Dry stream or wash	Río seco o aluvión
Well; Spring; Intermittent stream	Pozo; Manantial; Río intermitente
Intermittent lake; Navigable canal	Laguna intermitente; Canal navegable
Pier; Reef	Muelle; Arrecife
Dams: Masonry; Earthen	Presas: de fábrica; de tierra

HOJA SHEET 3263 I SERIE SERIES E752 EDICIÓN EDITION 1–DMA ZAPOTE

GRID NORTH / NORTE DE CUADRÍCULA

GRID CONVERGENCE 0°39' (12 MILS) FOR CENTER OF SHEET

CONVERGENCIA DE LA CUADRÍCULA 0°39' (12 MILÉSIMAS) PARA EL CENTRO DE LA HOJA

TO CONVERT A MAGNETIC AZIMUTH TO A GRID AZIMUTH ADD G-M ANGLE

TO CONVERT A GRID AZIMUTH TO A MAGNETIC AZIMUTH SUBTRACT G-M ANGLE

MAGNETIC NORTH / NORTE MAGNÉTICO

1980 G-M ANGLE 2° (40 MILS)
1980 *ÁNGULO C-M 2° (40 MILÉSIMAS)*


PARA CONVERTIR UN ACIMUT MAGNÉTICO A UN ACIMUT DE LA CUADRÍCULA SUMESE EL ÁNGULO C-M

PARA CONVERTIR UN ACIMUT DE LA CUADRÍCULA A UN ACIMUT MAGNÉTICO RESTESE EL ÁNGULO C-M


ELEVATION GUIDE
GUÍA DE ELEVACIÓN



ADJOINING SHEETS
HOJAS ADYACENTES

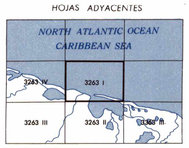

BOUNDARIES
LÍMITES

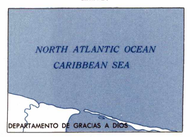

GLOSSARY GLOSARIO

Alineamiento a proximado. Alin. aprox.	approximate alignment
Barra	sand bar
Departamento	first-order administrative division
Laguna	lake
Navegable	navigable
Río	stream
Ruta de navegación	navigation route
Sabana	flatland

LIMITED DISTRIBUTION Distribution authorized to DoD, IAW 10 U.S.C §§130 & 455. Release authorized to U.S. DoD contractors, IAW 48 C.F.R. §252.245-7000. Refer other requests to Headquarters, NIMA, ATTN: Release Officer, Stop P-25. Destroy as "For Official Use Only." Removal of this caveat is prohibited.

THIS MAP IS RED-LIGHT READABLE

NSN 7643014015450 ED. NO. 001

NIMA REF. NO. E752X32631